

LYNK & CO

DESSIER TECHNIQUE

Stand: LYNK & CO

Stand No: 51 A 32

Hall: 5.1

Surface: 368 M2

Dates de l'exposition: Du 12 au 18 Octobre 2026

Le Mondial de l'Auto, 2026


Porte de Versailles- Paris



Stand_ LYNK & CO_ le Mondial de l'Auto 2026
23/09/2026
Version _FINAL.1


Name	Page
POSITION DU STAND	1
PLAN GENARAL RDC	2A
PLAN GENARAL 1E ETAGE	2B
PLAN SOL RDC	3A
PLAN SOL 1E ETAGE	3B
PLAN CLOISON RDC	4
PLAN HABILLAGE DE STAND	5
PLAN VELUM	6
ELEVATION A	7
ELEVATION B	8
ELEVATION C	9
ELEVATION D	10
PLAN ELINGUES	11
PLAN TABLEAU ELECTRIQUE	12
PLAN ELECTRIQUE RDC	13A
PLAN ELECTRIQUE 1E ETAGE	13B
PLAN ELECTRIQUE 2EME ETAGE	13C
PLAN ELECTRIQUE TRUSS	13D
PLAN Position des voitures et meubles	14
MEUBLE-BAR	15
MEUBLE BORNE ANIMATION	16

ALLÉE
(Côté du Stand Tesla)

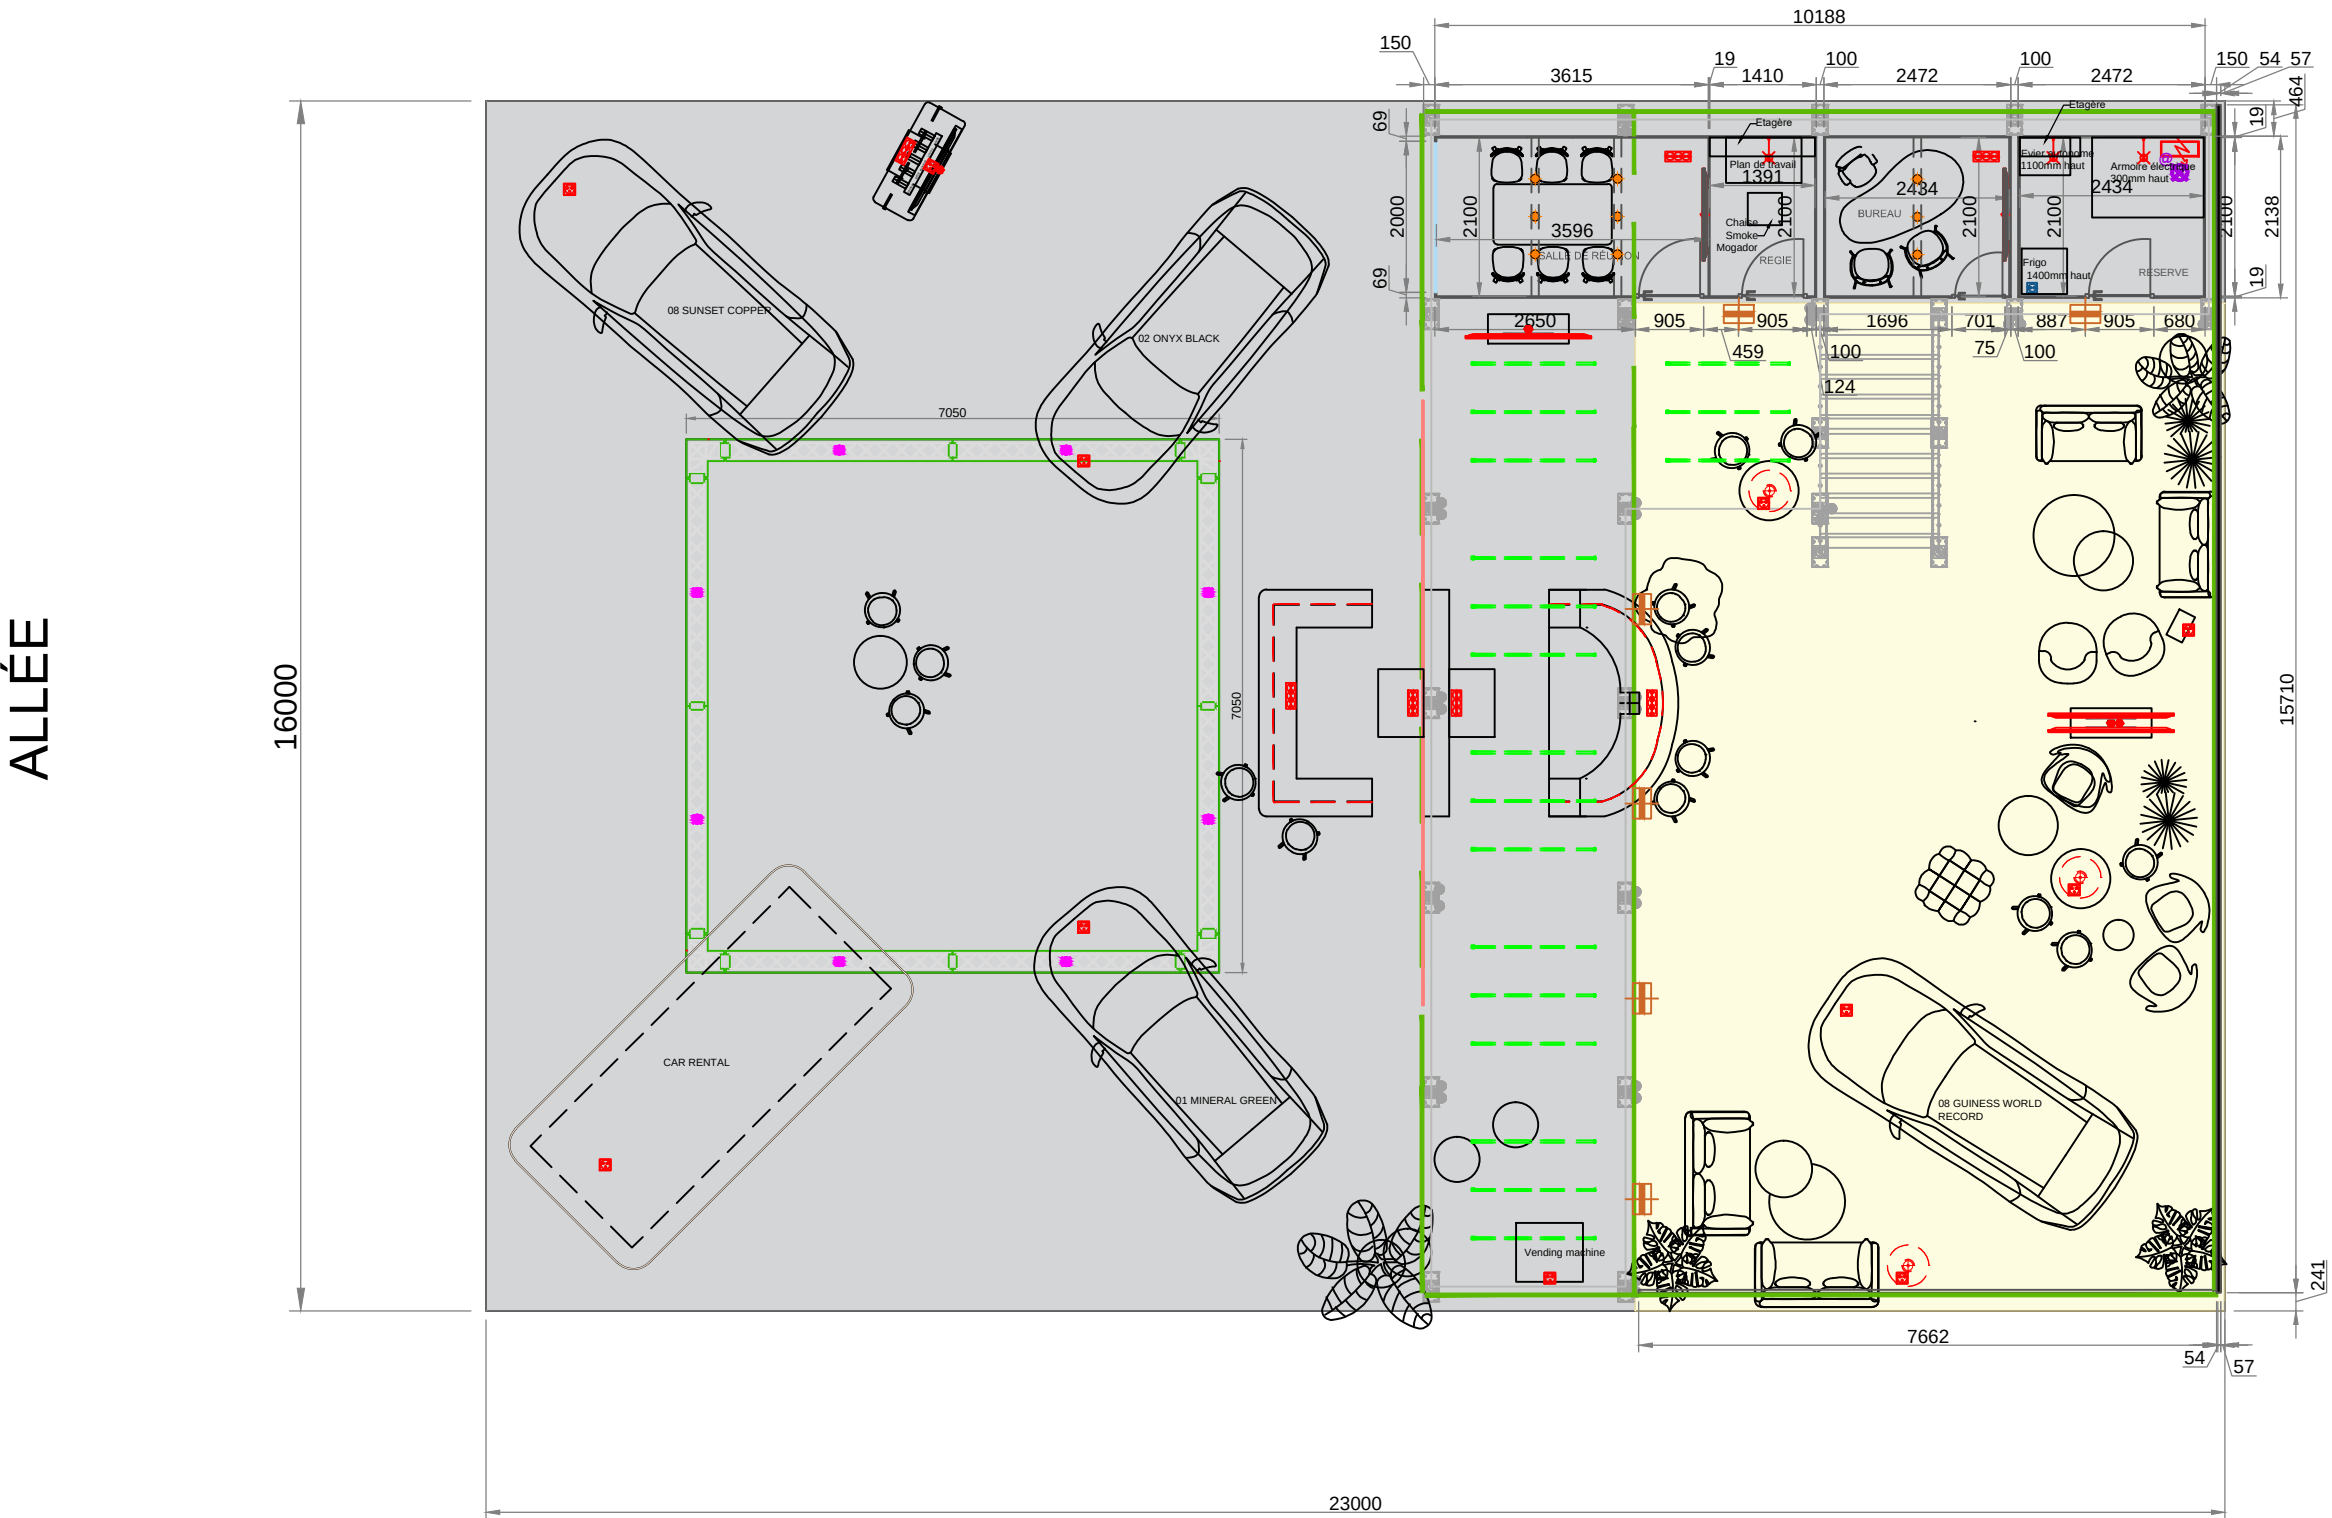


ALLÉE
(Côté du Stand Electric box)

ALLÉE
(Côté du Stand Tesla)

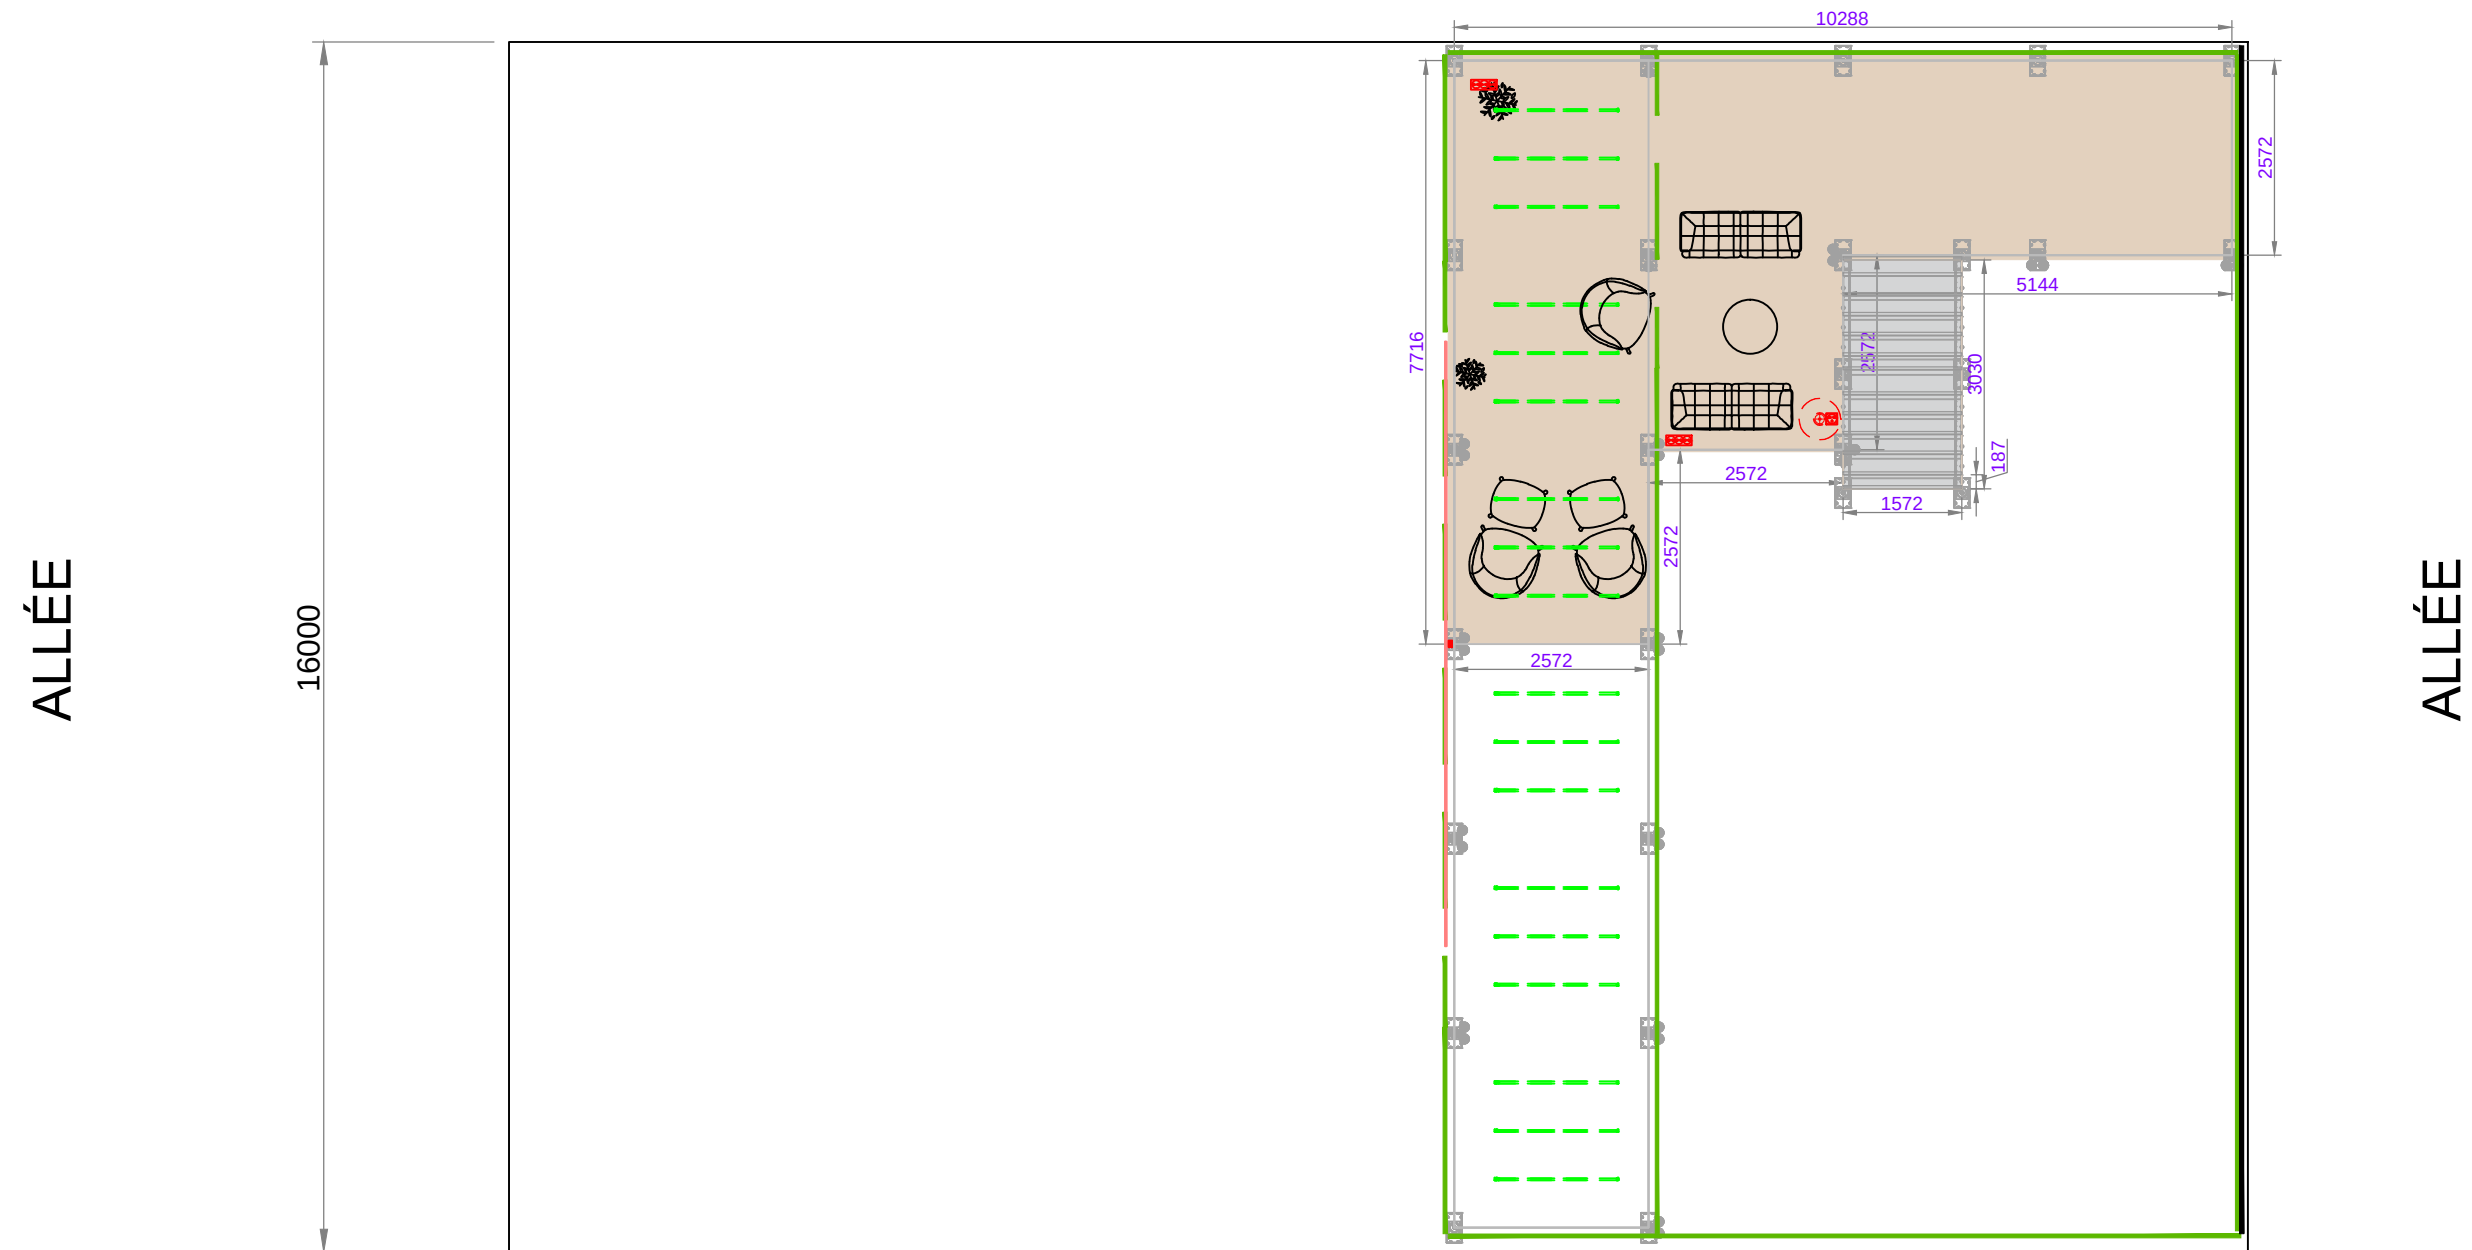

ALLÉE
(Côté du Stand Electric box)


ALLÉE (Côté du Stand Tesla)

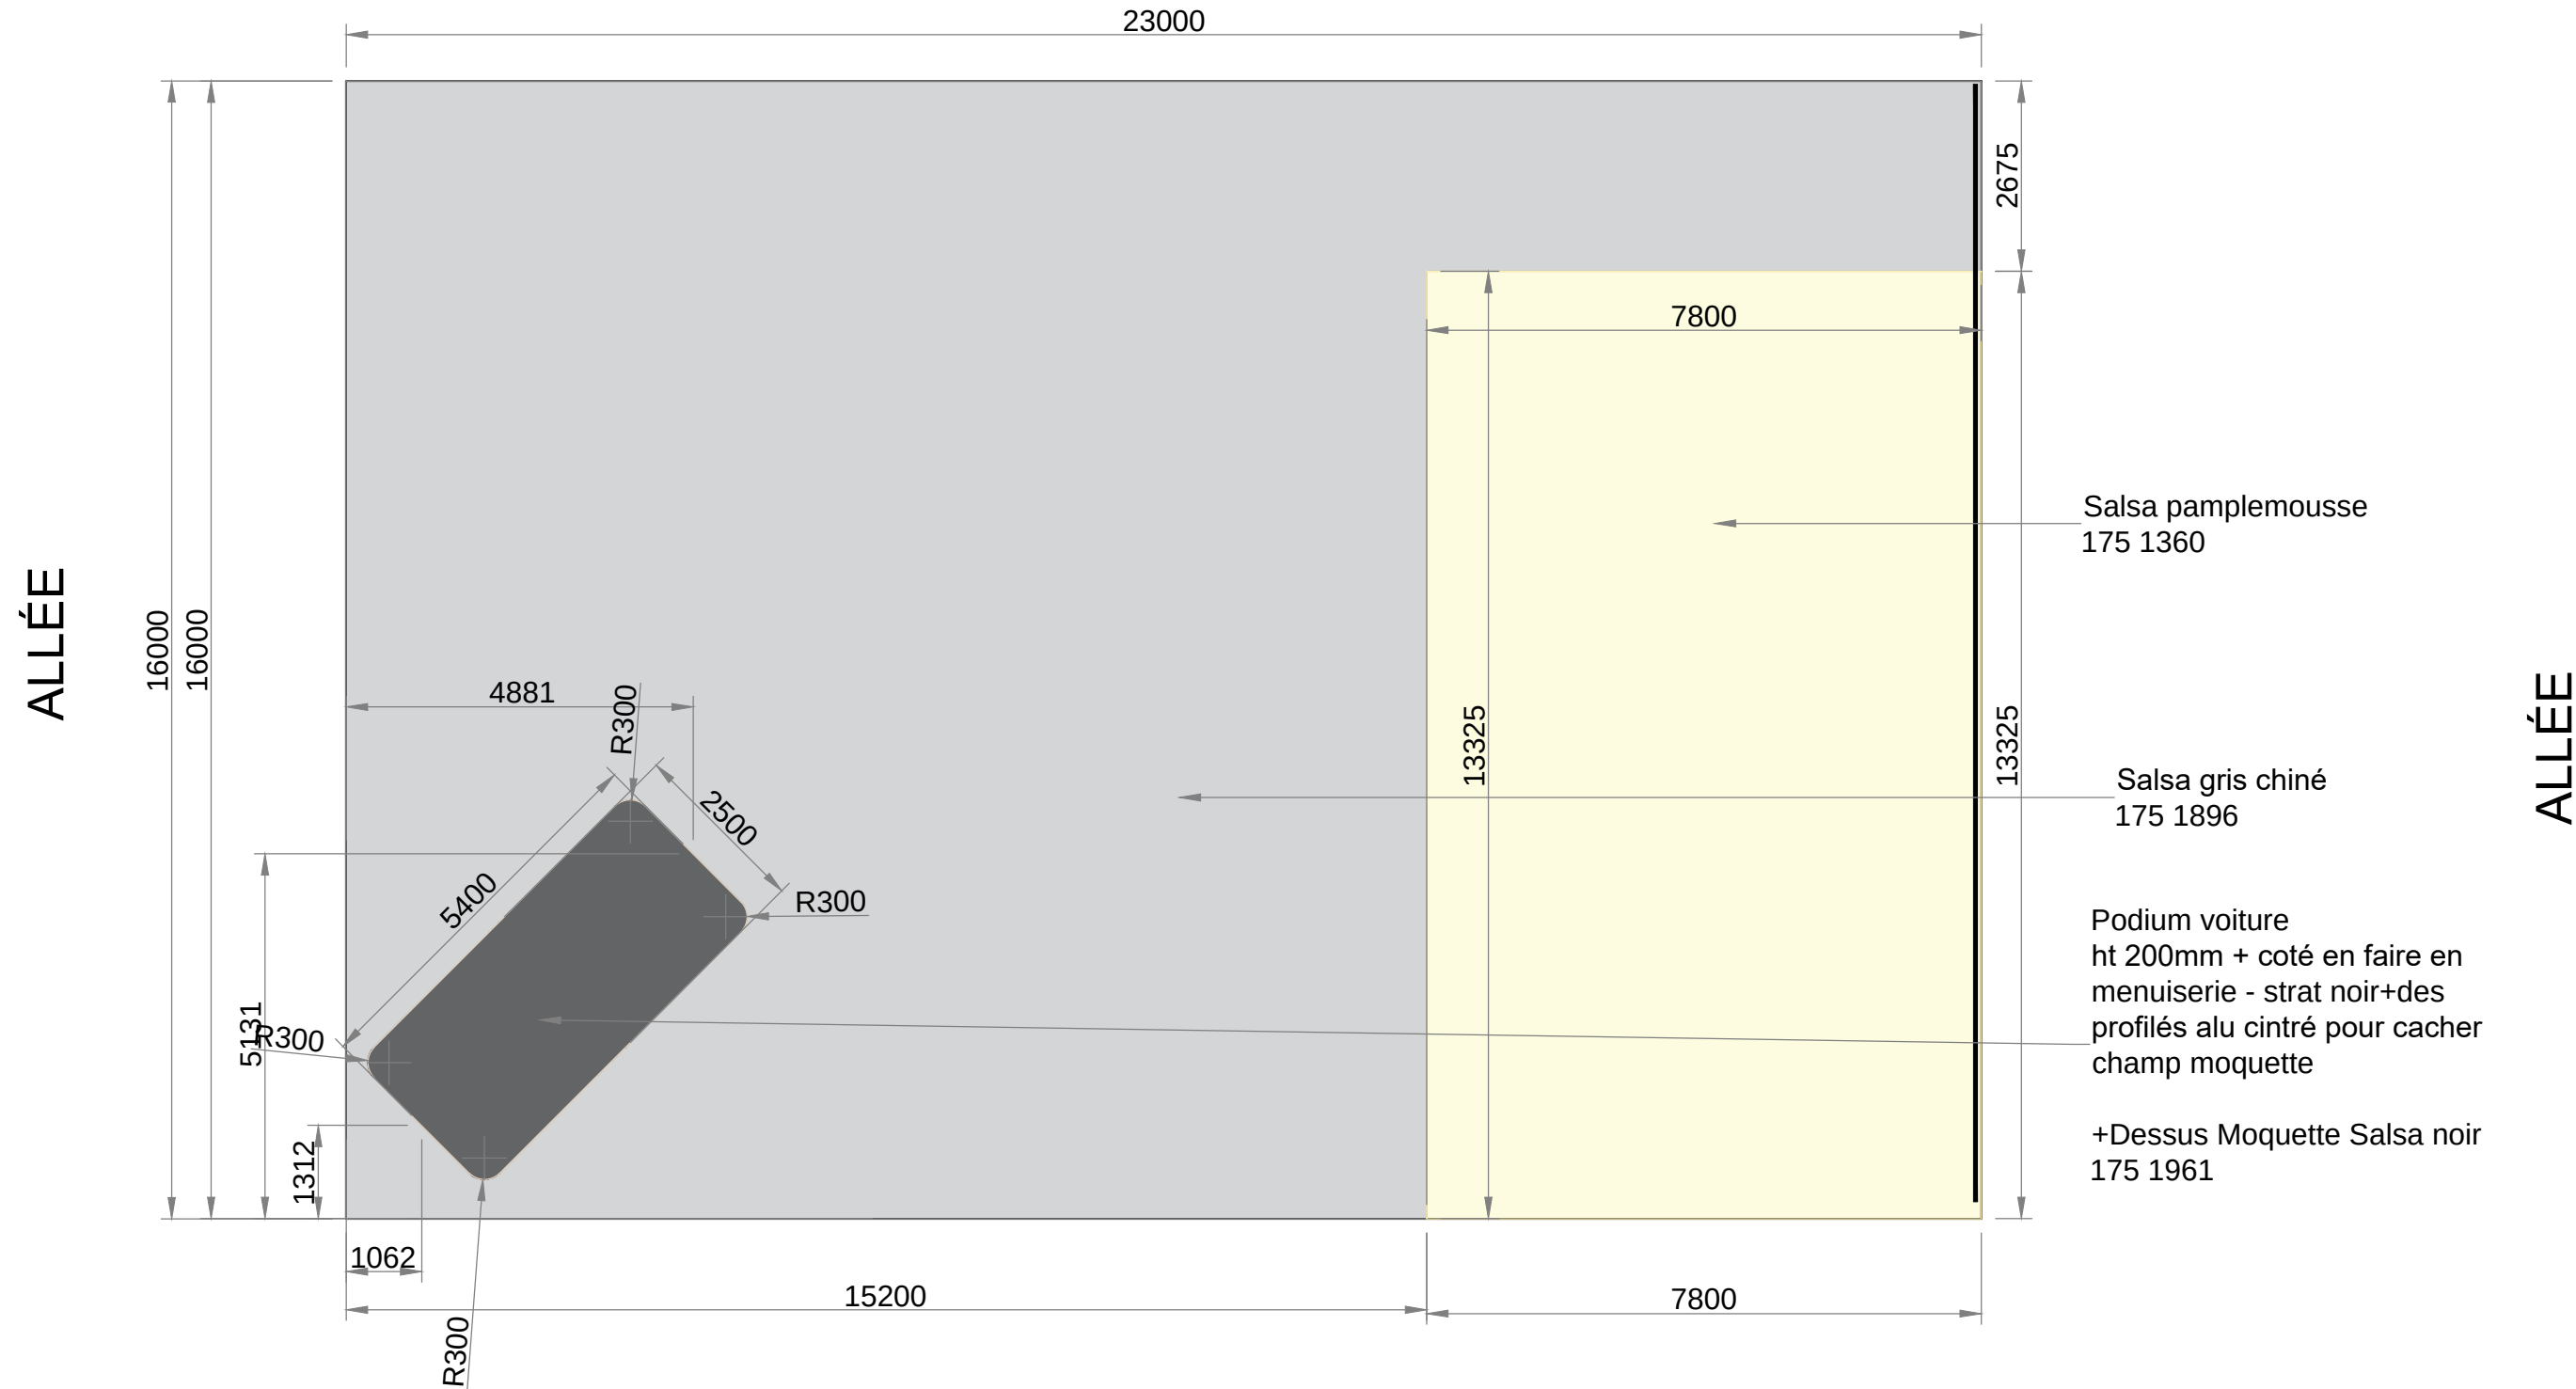

ALLÉE (Côté du Stand Electric box)

ALLÉE
(Côté du Stand Tesla)

ALLÉE

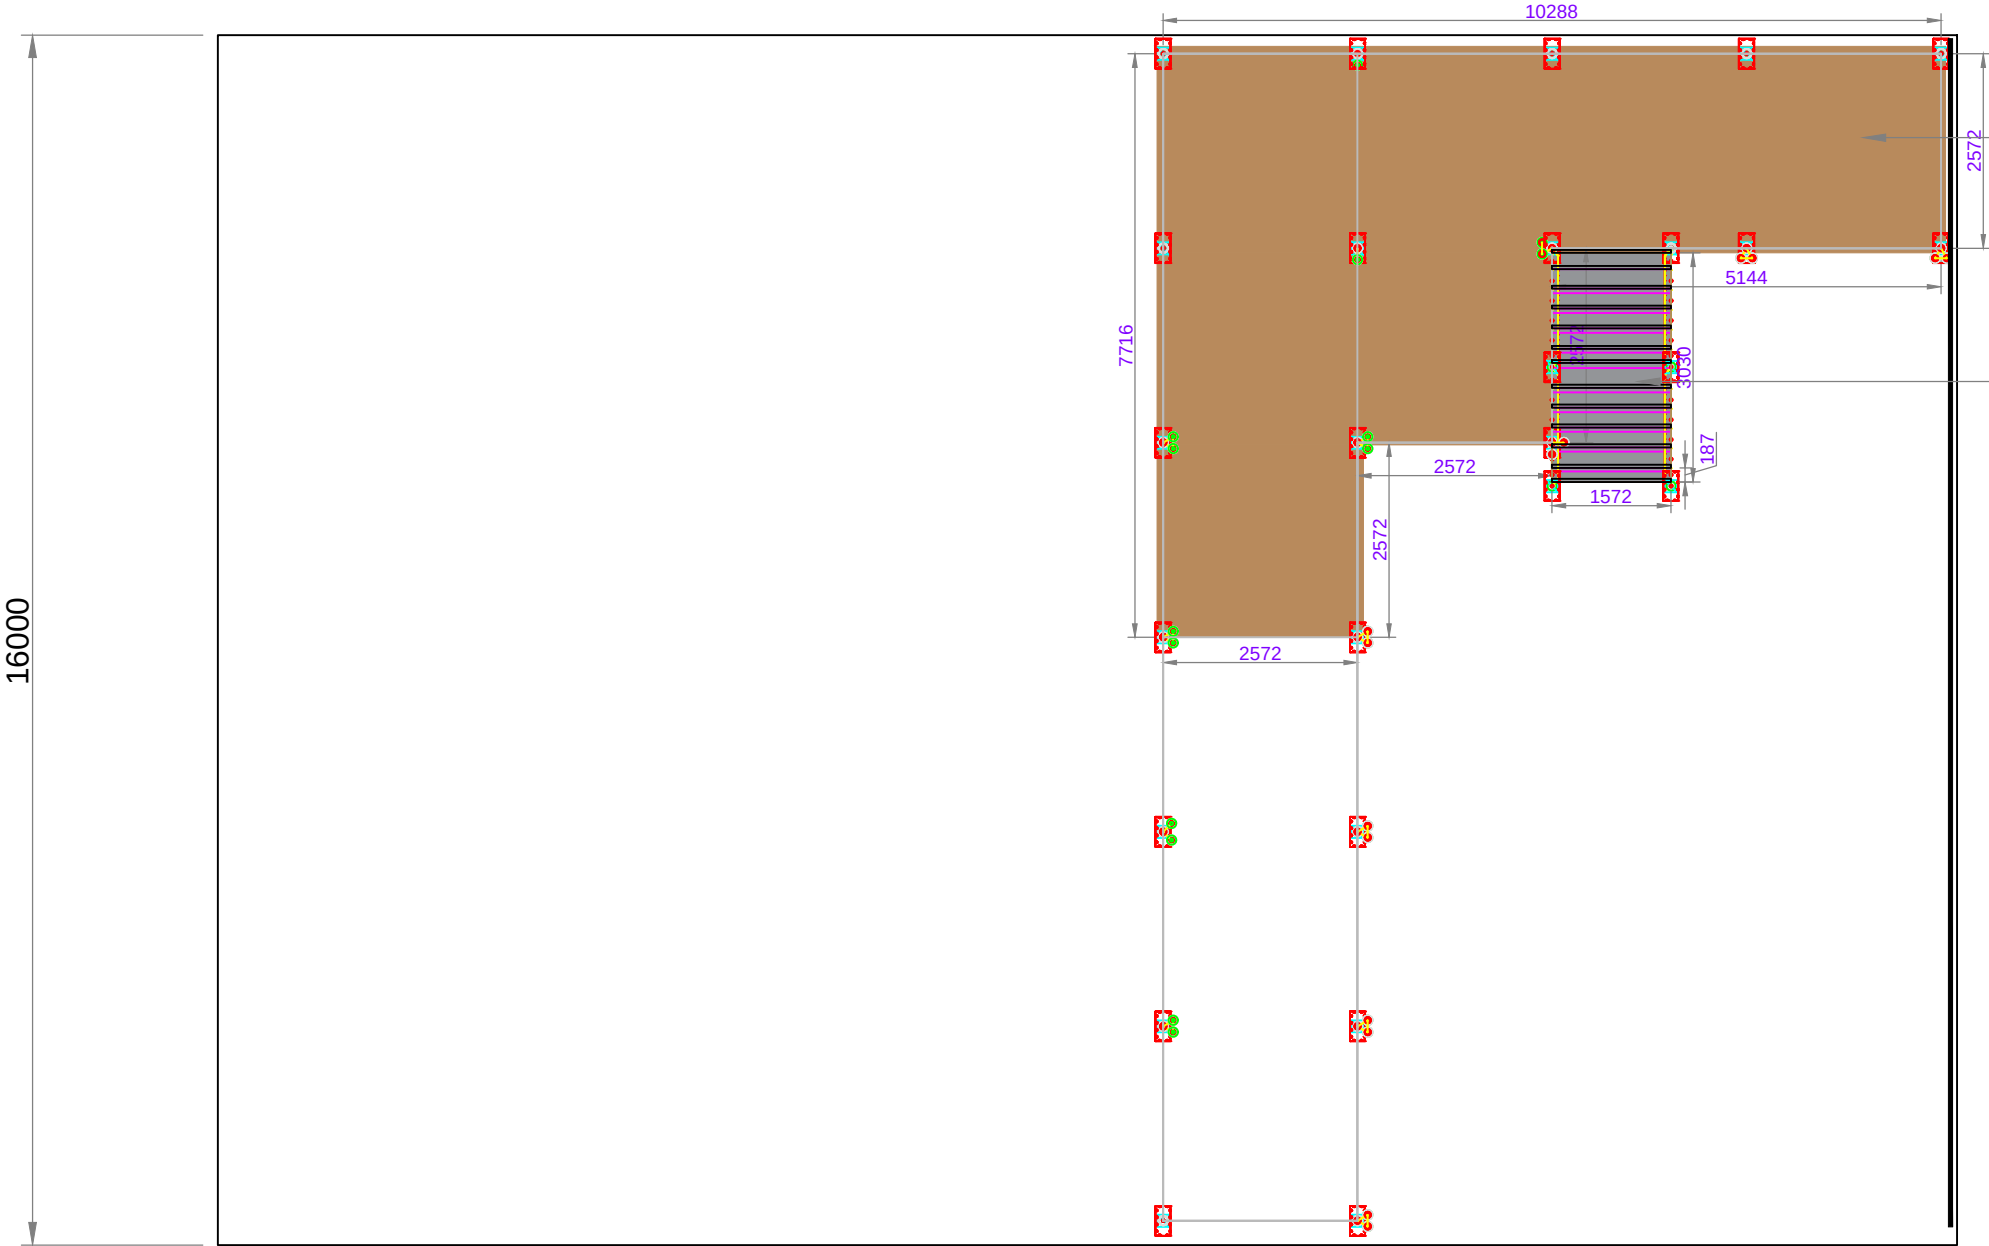

Plancher mela Egger Chromix Argent F638
ST10

Moquette Salsa gris foncé 175 1896


13 fois plats de marche escalier
1572mm x 187mm

+13 fois nez de marche sur l'escalier
1572mm x 40mm x 25 mm

ALLÉE

ALLÉE
(Côté du Stand Electric box)

(Côté du Stand Tesla)

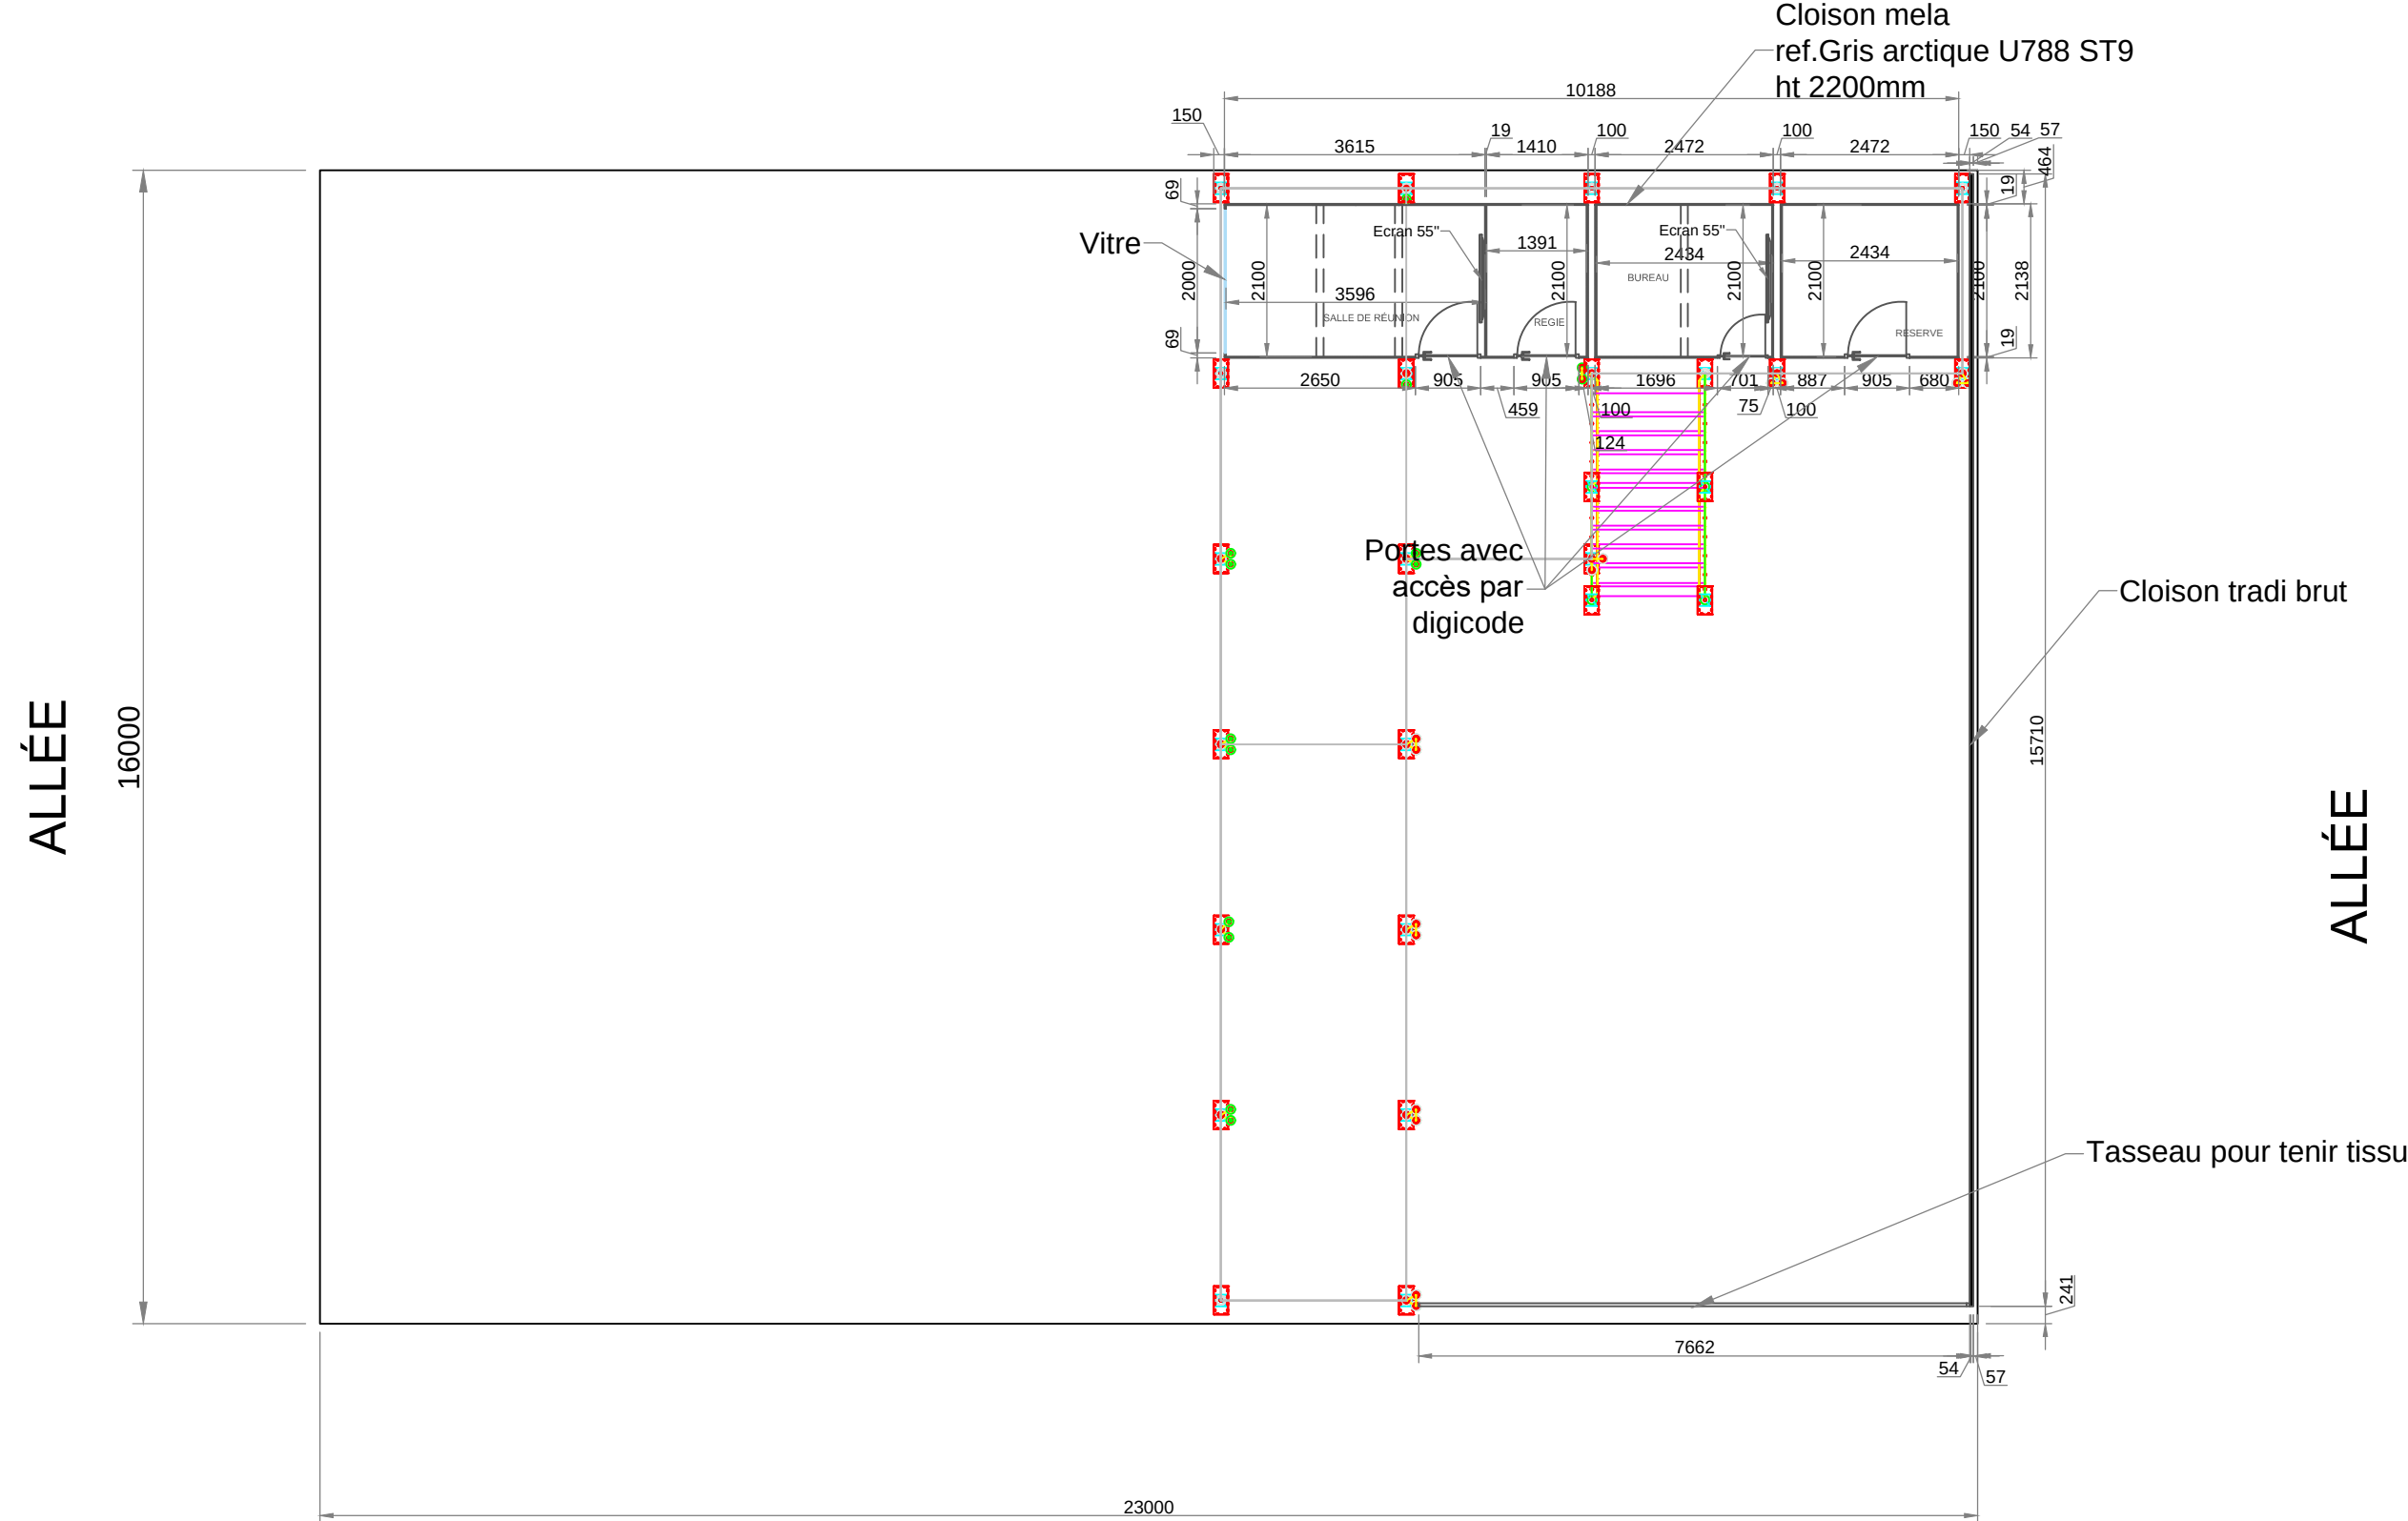

(Côté du Stand Electric box)




108 avenue Henri Barbusse
92600 Asnières-sur-Seine, France







Nom de stand: **LYNK & CO**
Numéro de stand: 51 A 32
Surface: **368m2**

LYNK & CO / DESSIN TECHNIQUE	
PLAN CLOISON rdc	
Le Mondial de l'Auto, 2026	Dates de l'exposition : 12-18 OCTOBRE 2026
	Porte de Versailles/ Hall-5.1


(Côté du Stand Tesla)

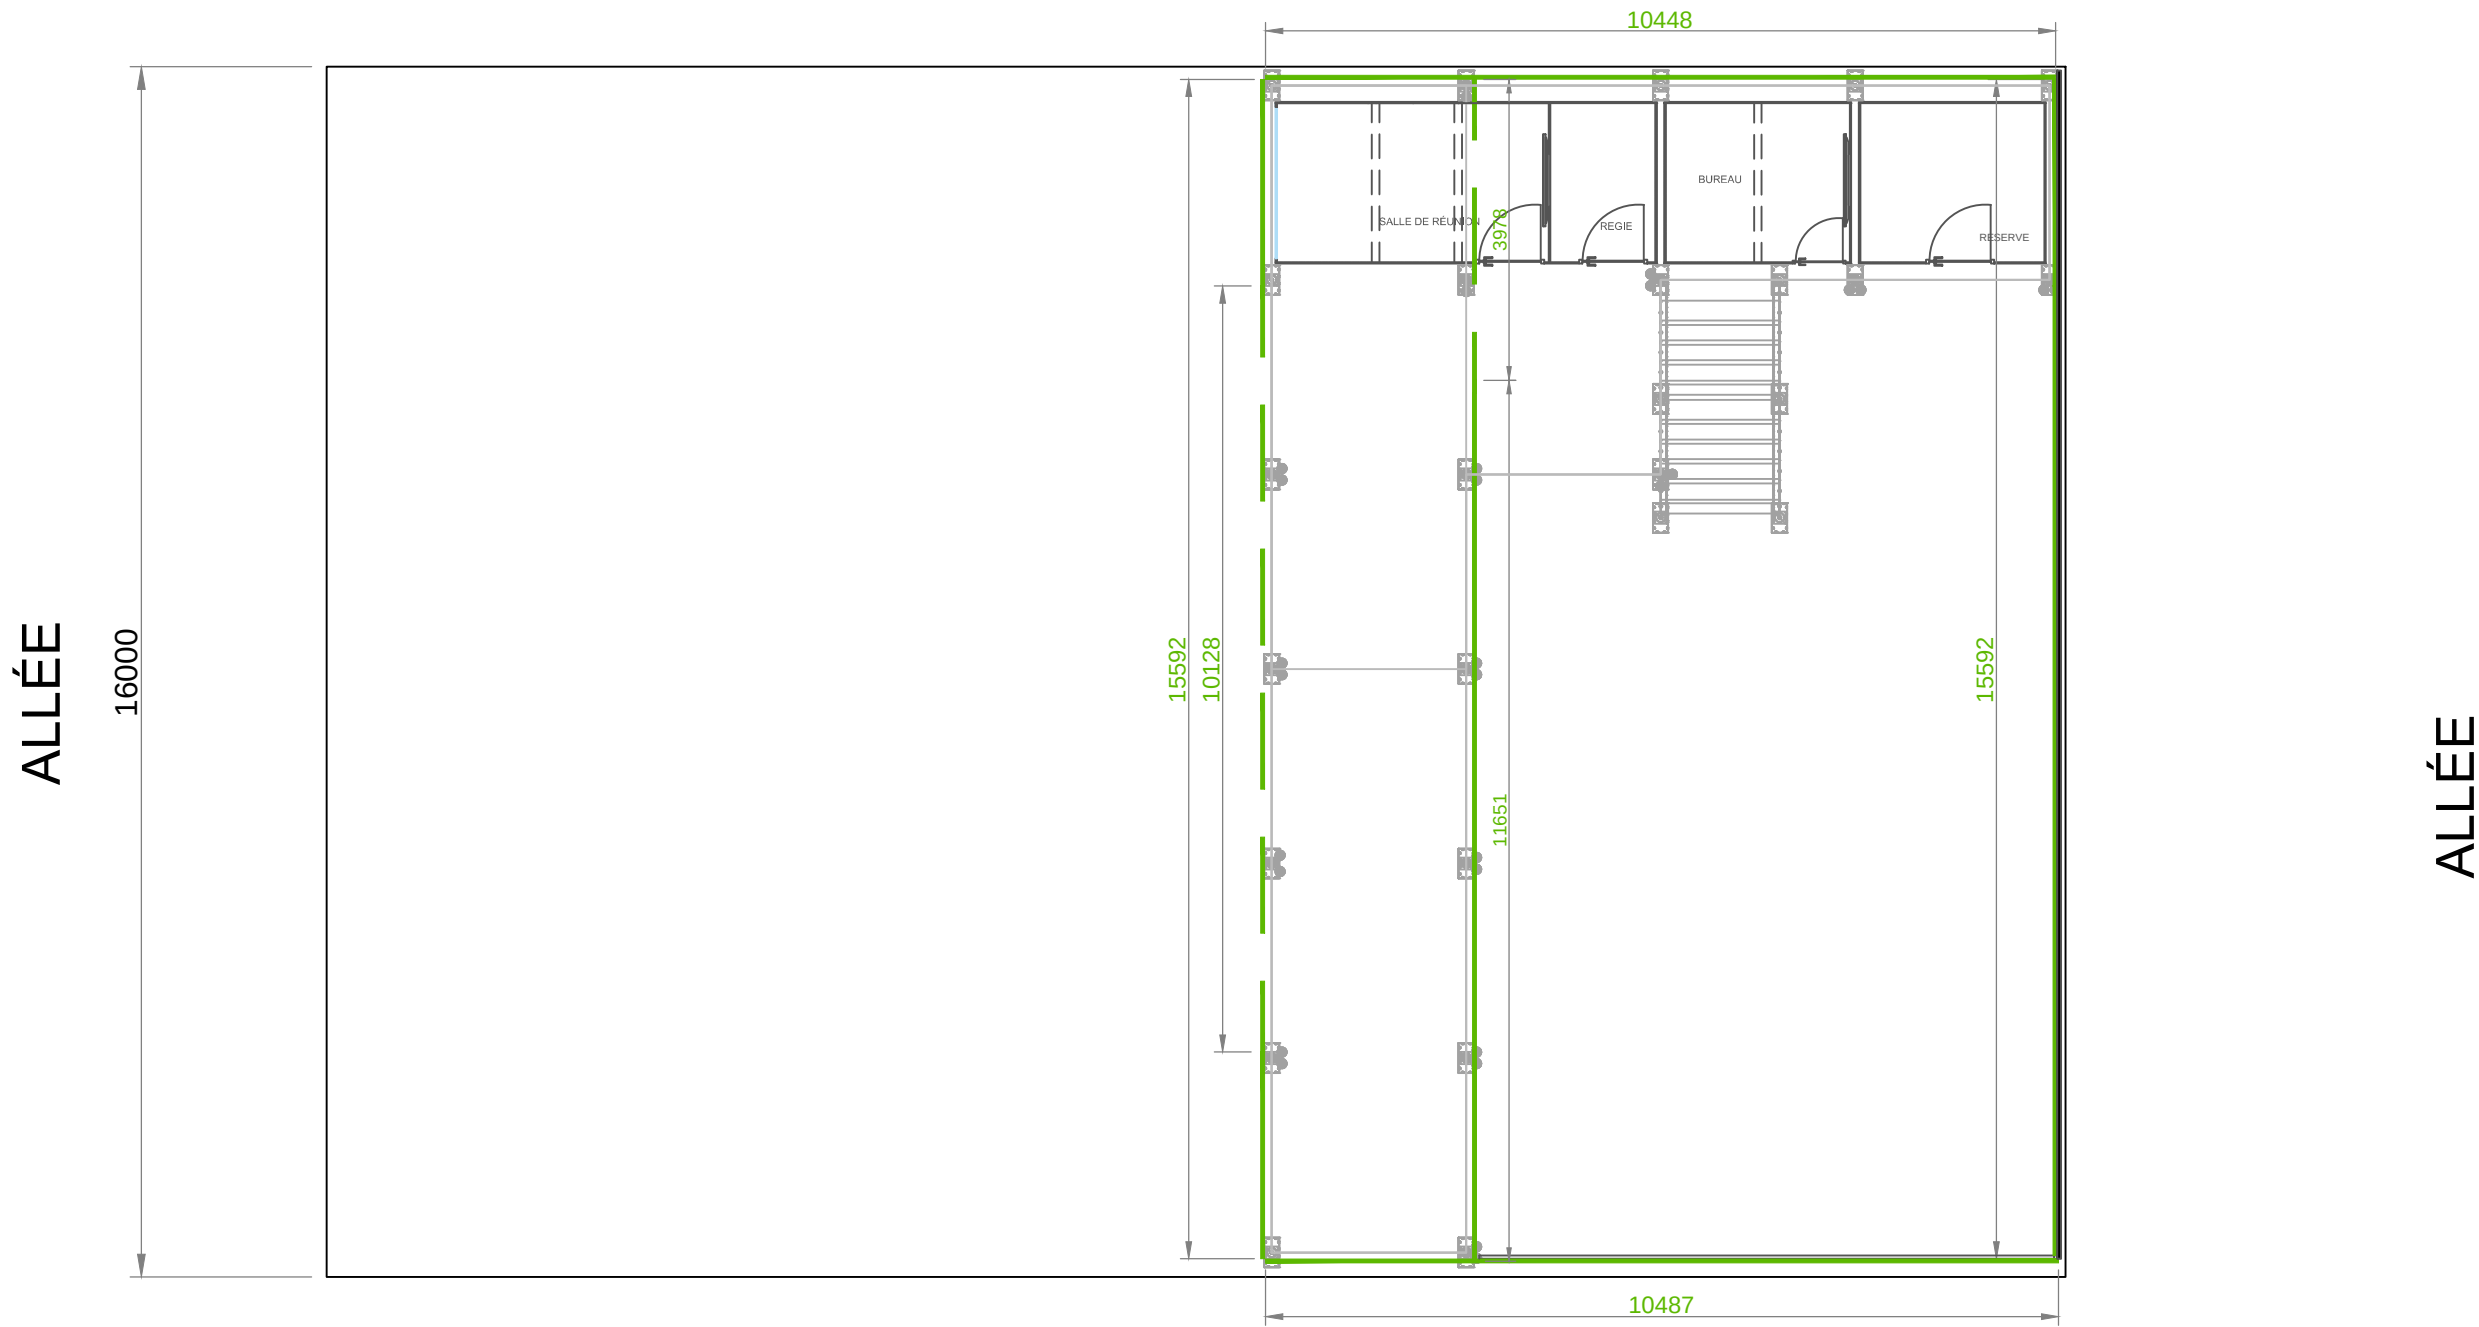

(Côté du Stand Electric box)

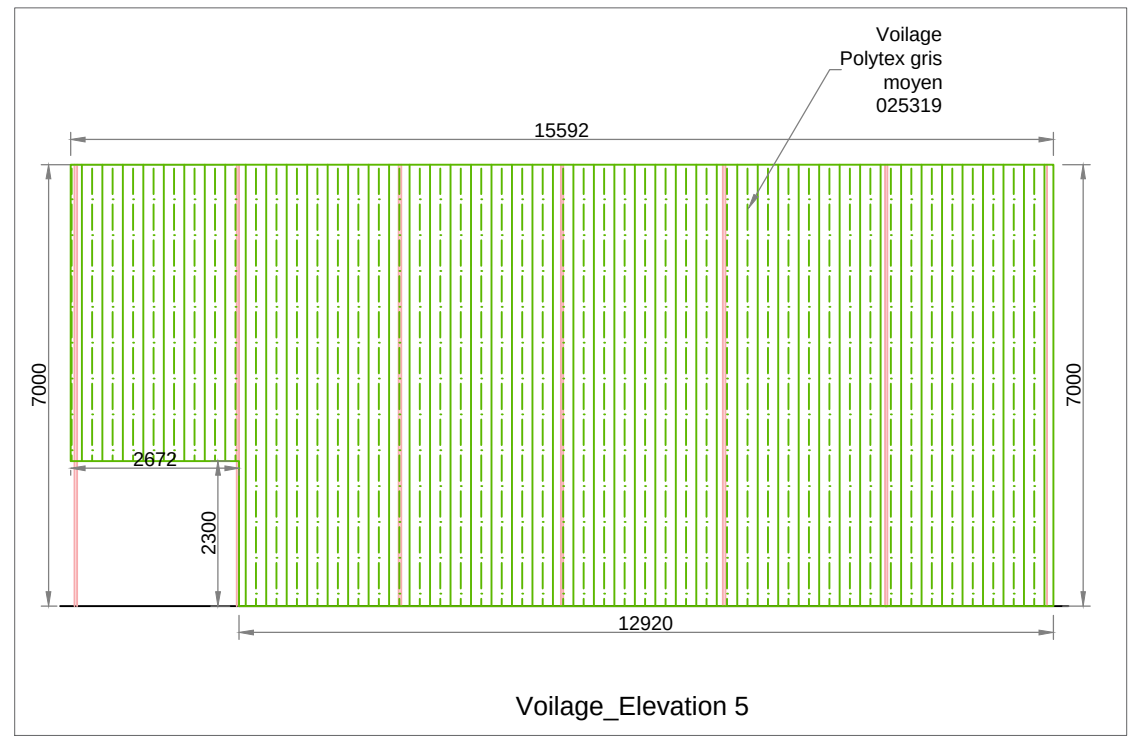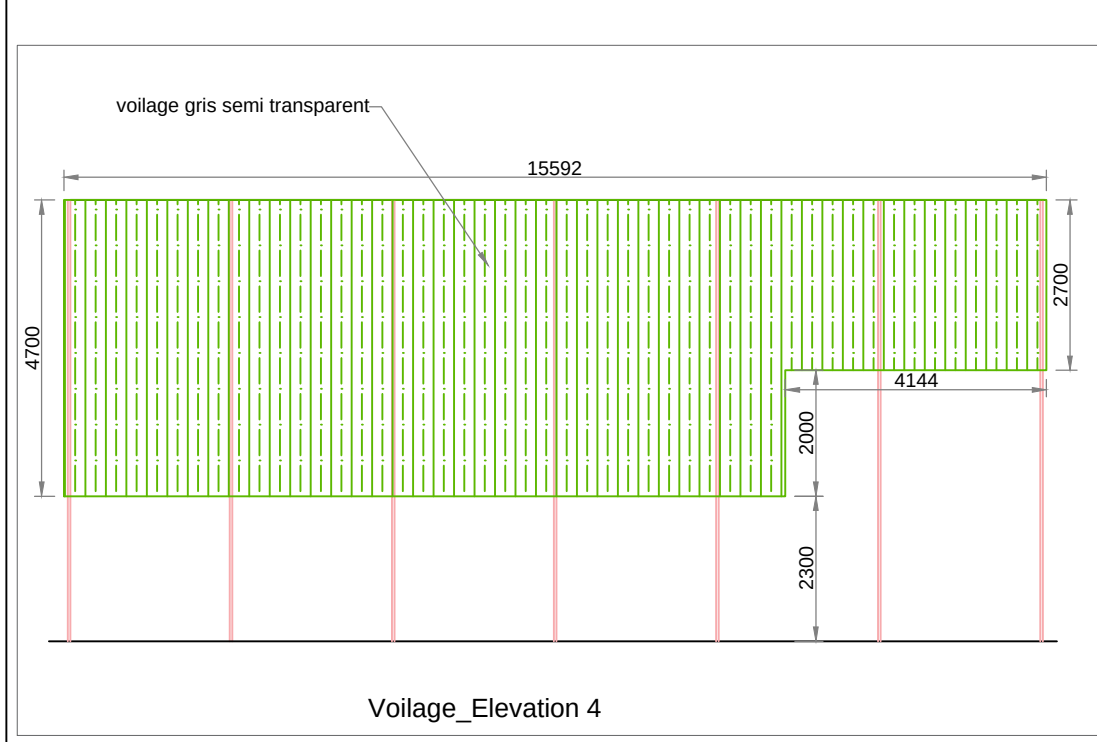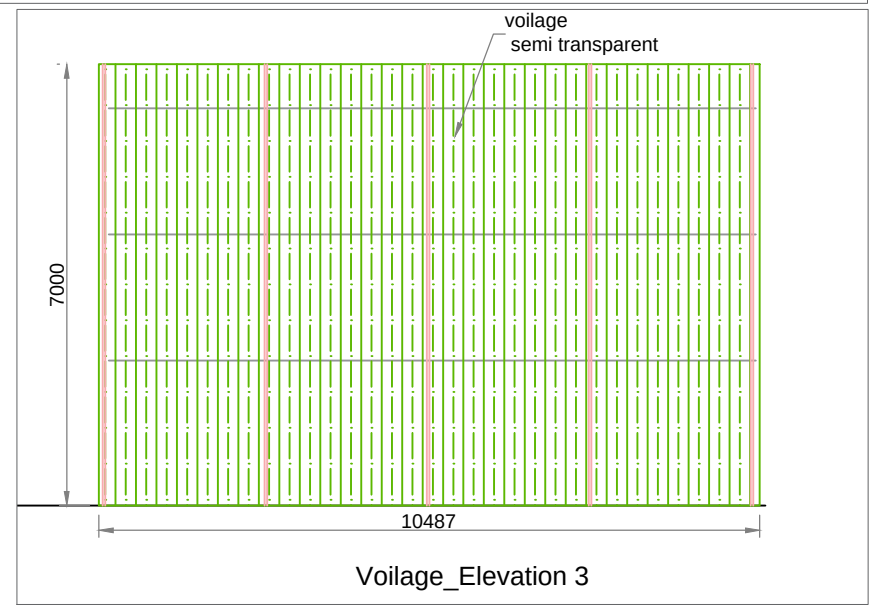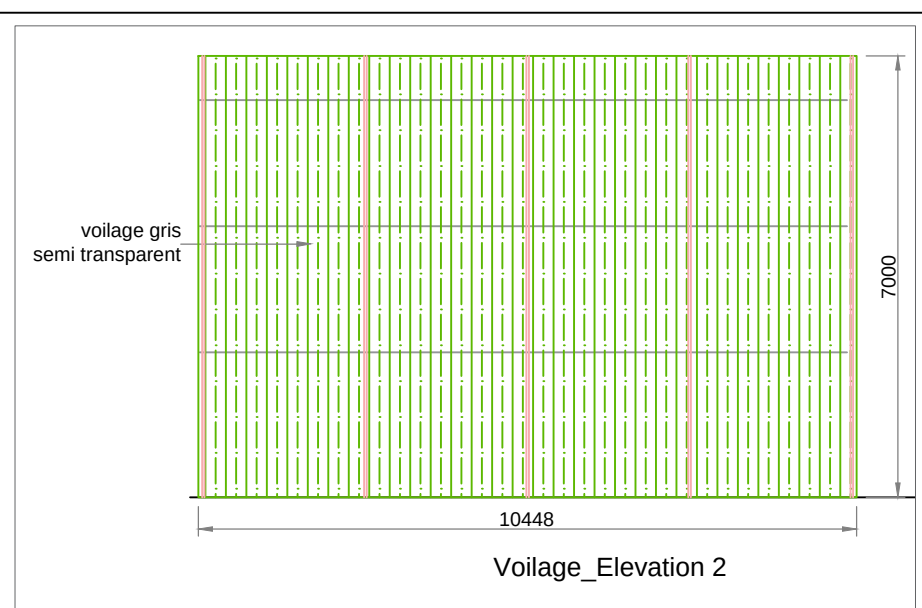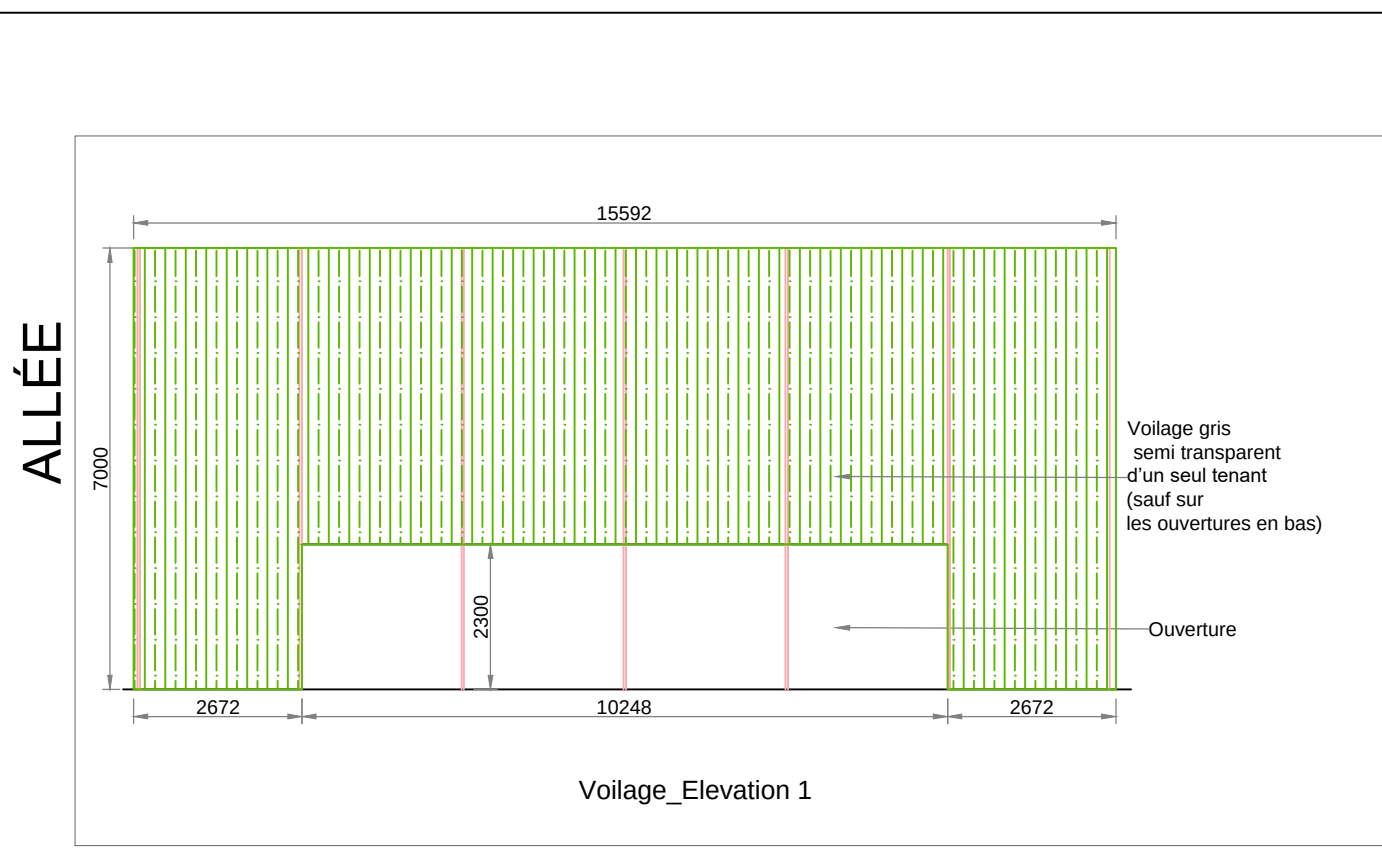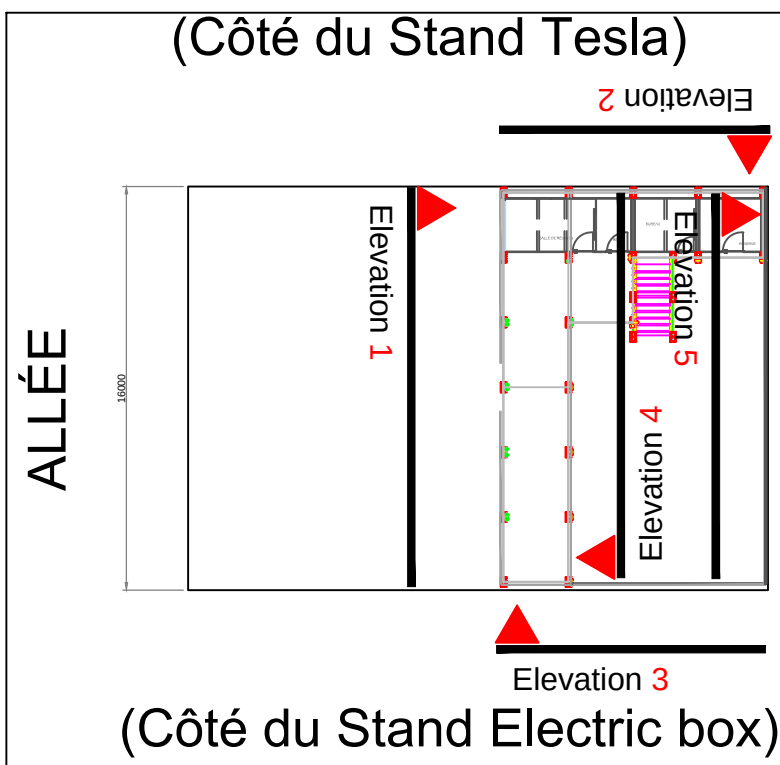




(Côté du Stand Tesla)

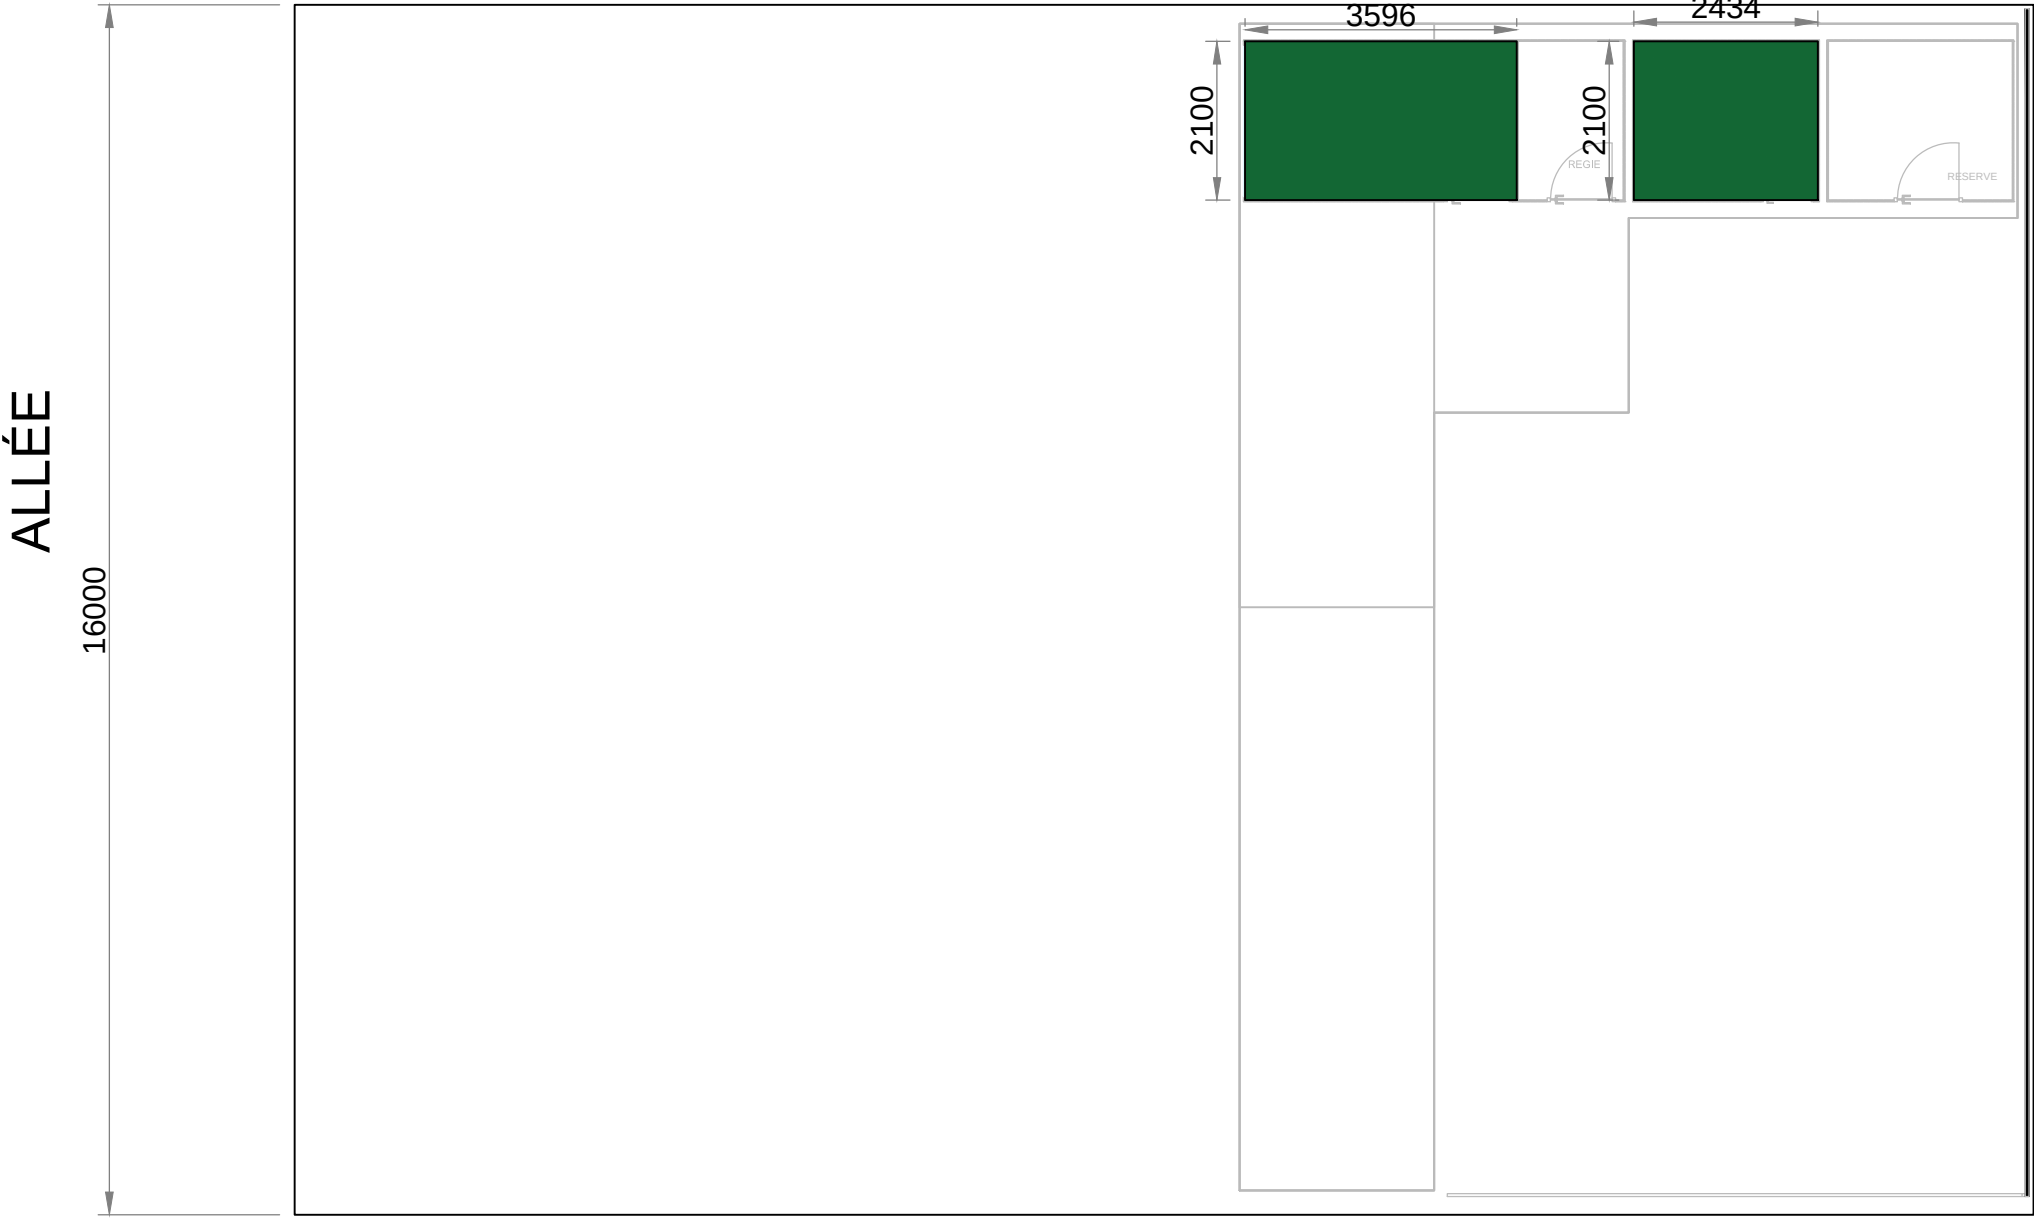

ALLÉE

 Vélum blanc

(Côté du Stand Electric box)

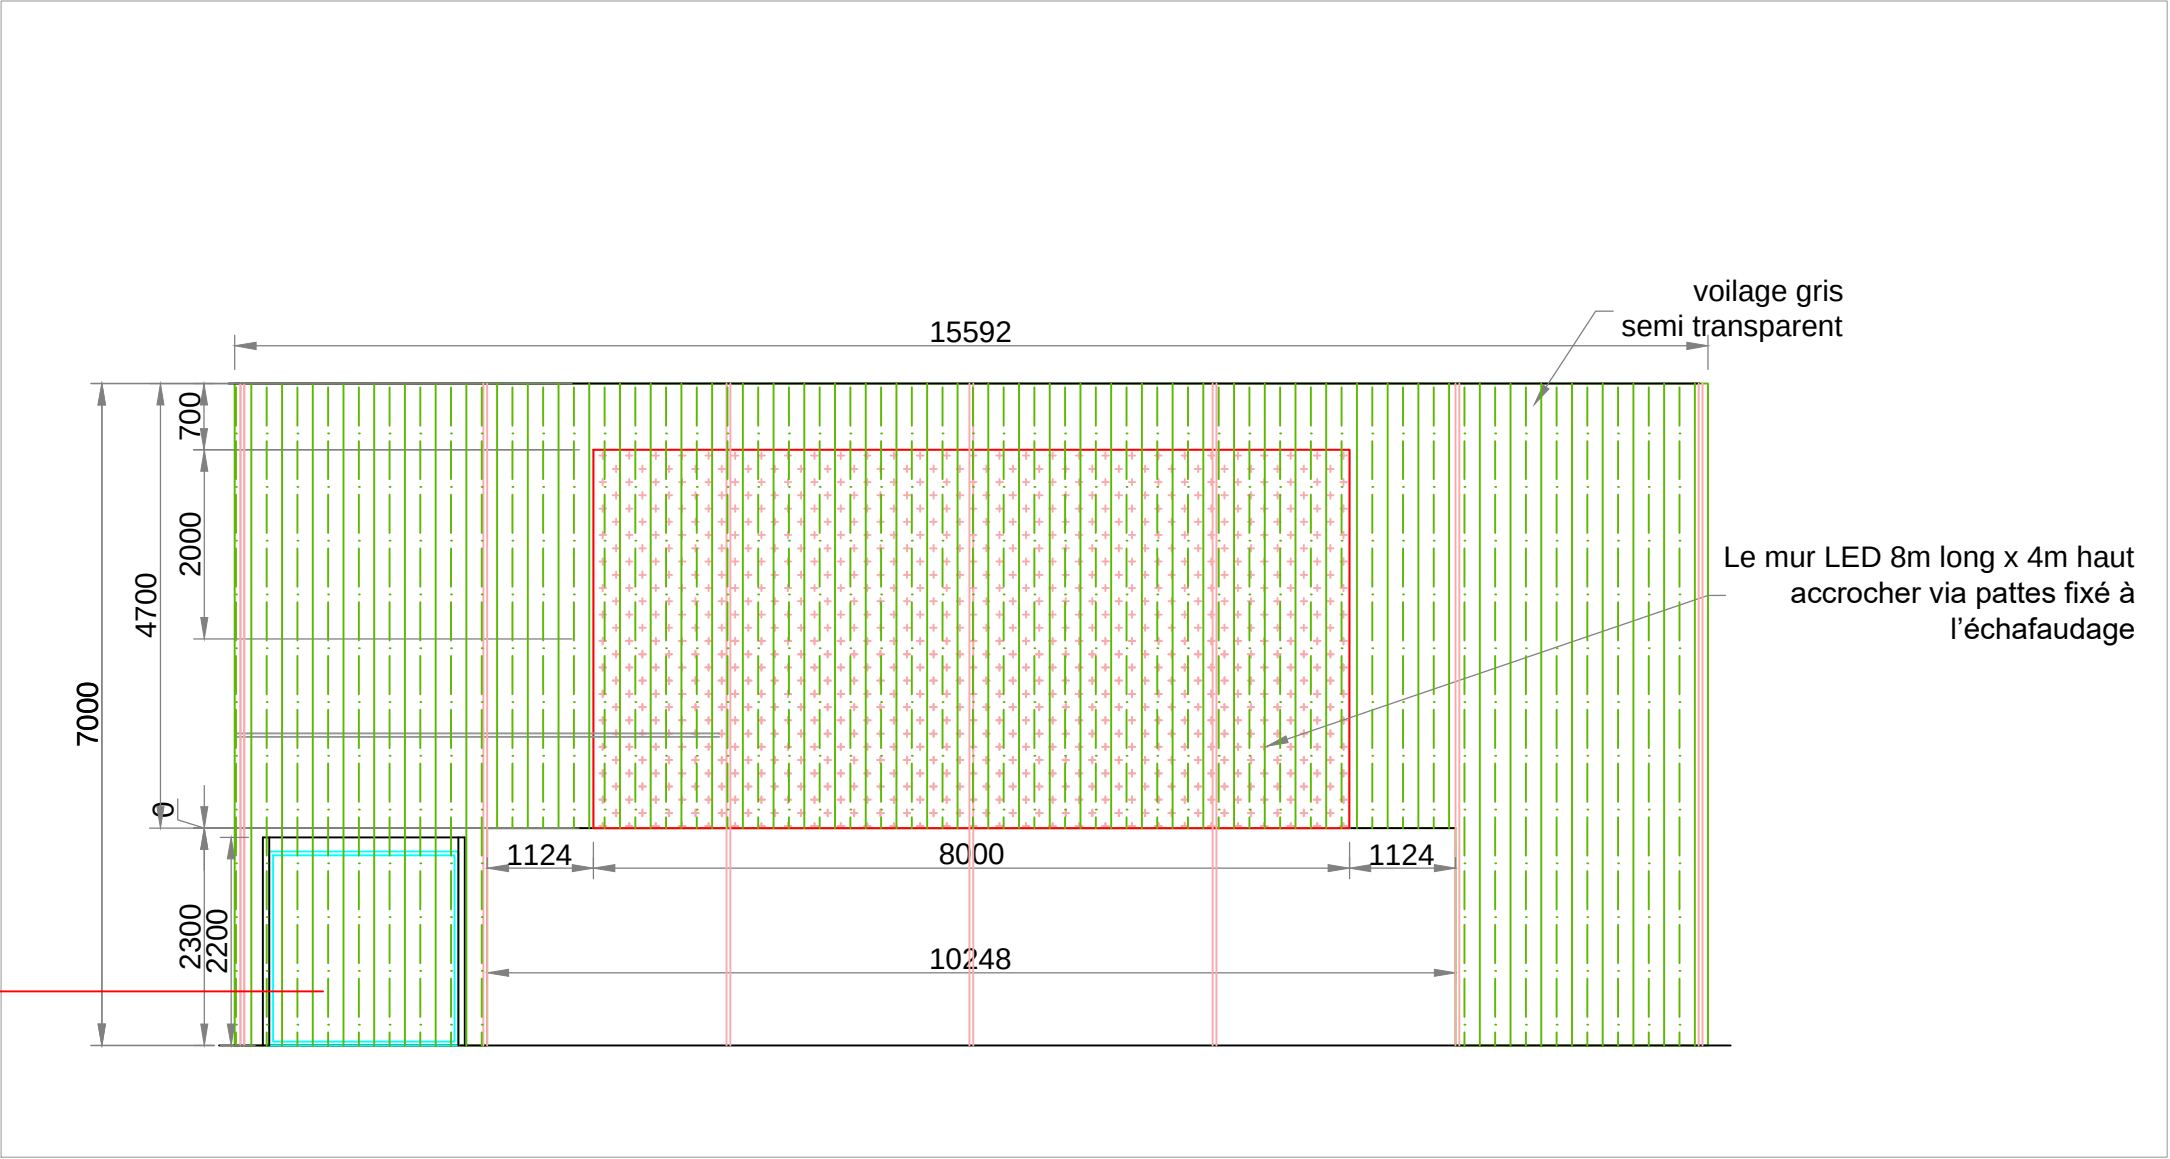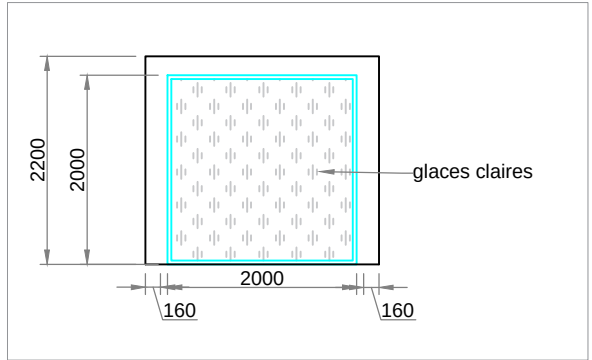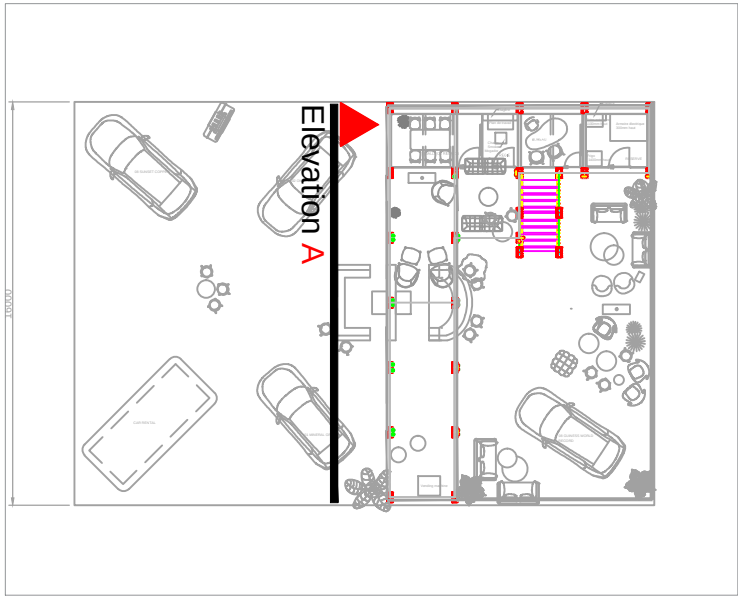


ELEVATION A




108 avenue Henri Barbusse
92600 Asnières-sur-Seine, France

Nom de stand: **LYNK & CO**
Numéro de stand: 51 A 32
Surface: **368m2**



LYNK & CO / DESSIN TECHNIQUE	
ELEVATION A	
Le Mondial de l'Auto, 2026	Dates de l'exposition : 12-18 OCTOBRE 2026
	Porte de Versailles/ Hall-5.1

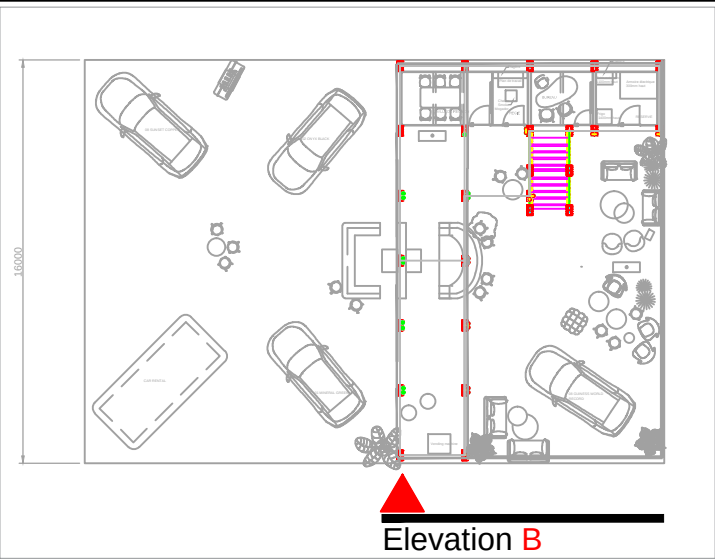



Elevation B

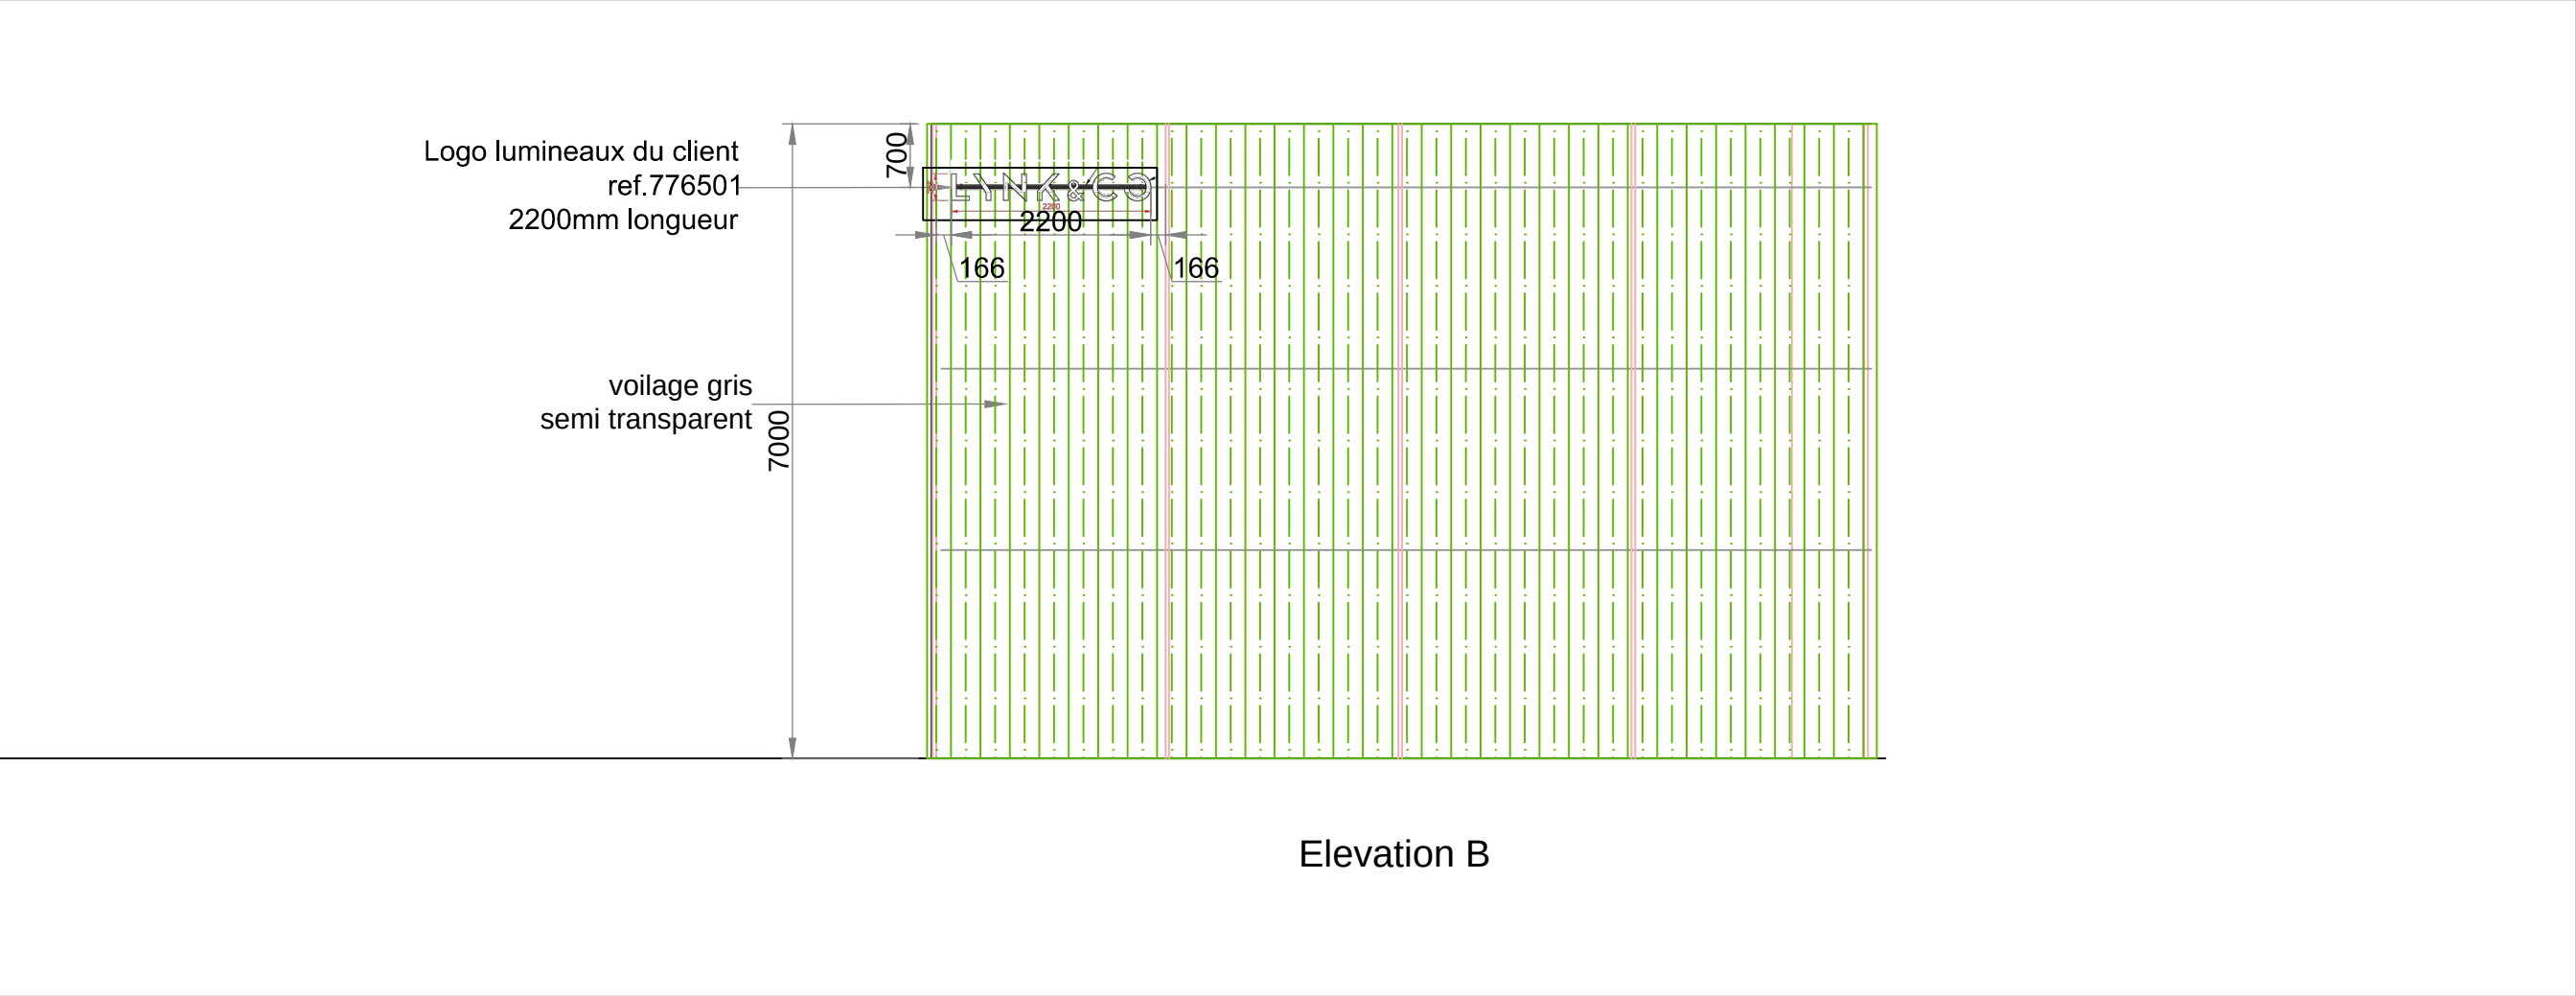

ELEVATION B

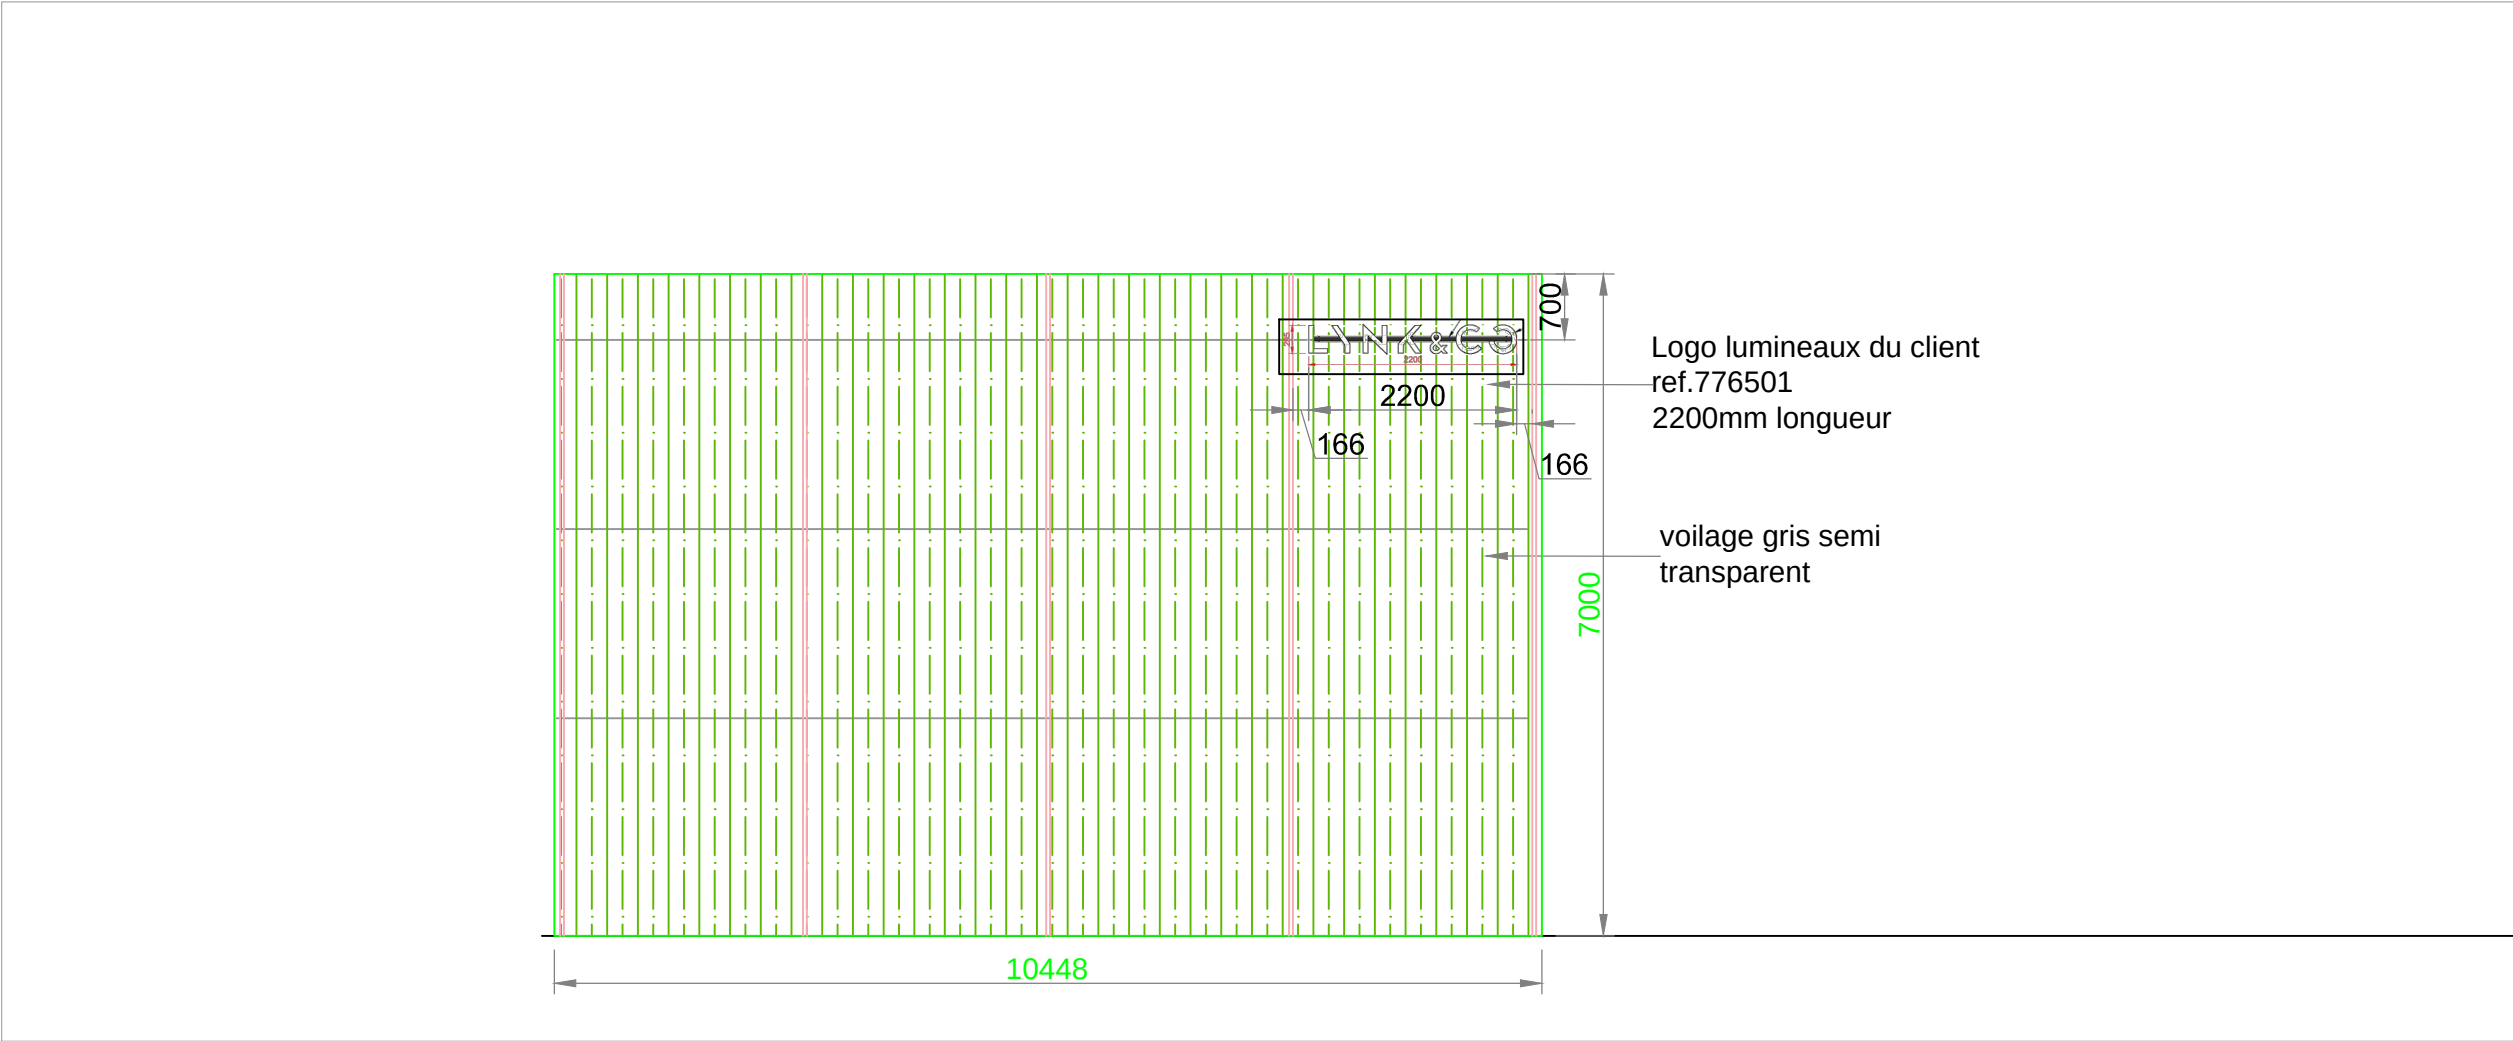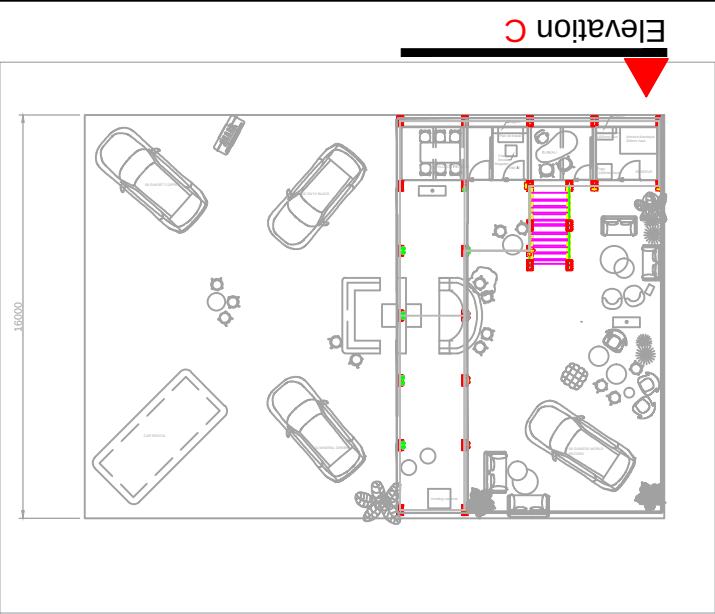

ELEVATION C

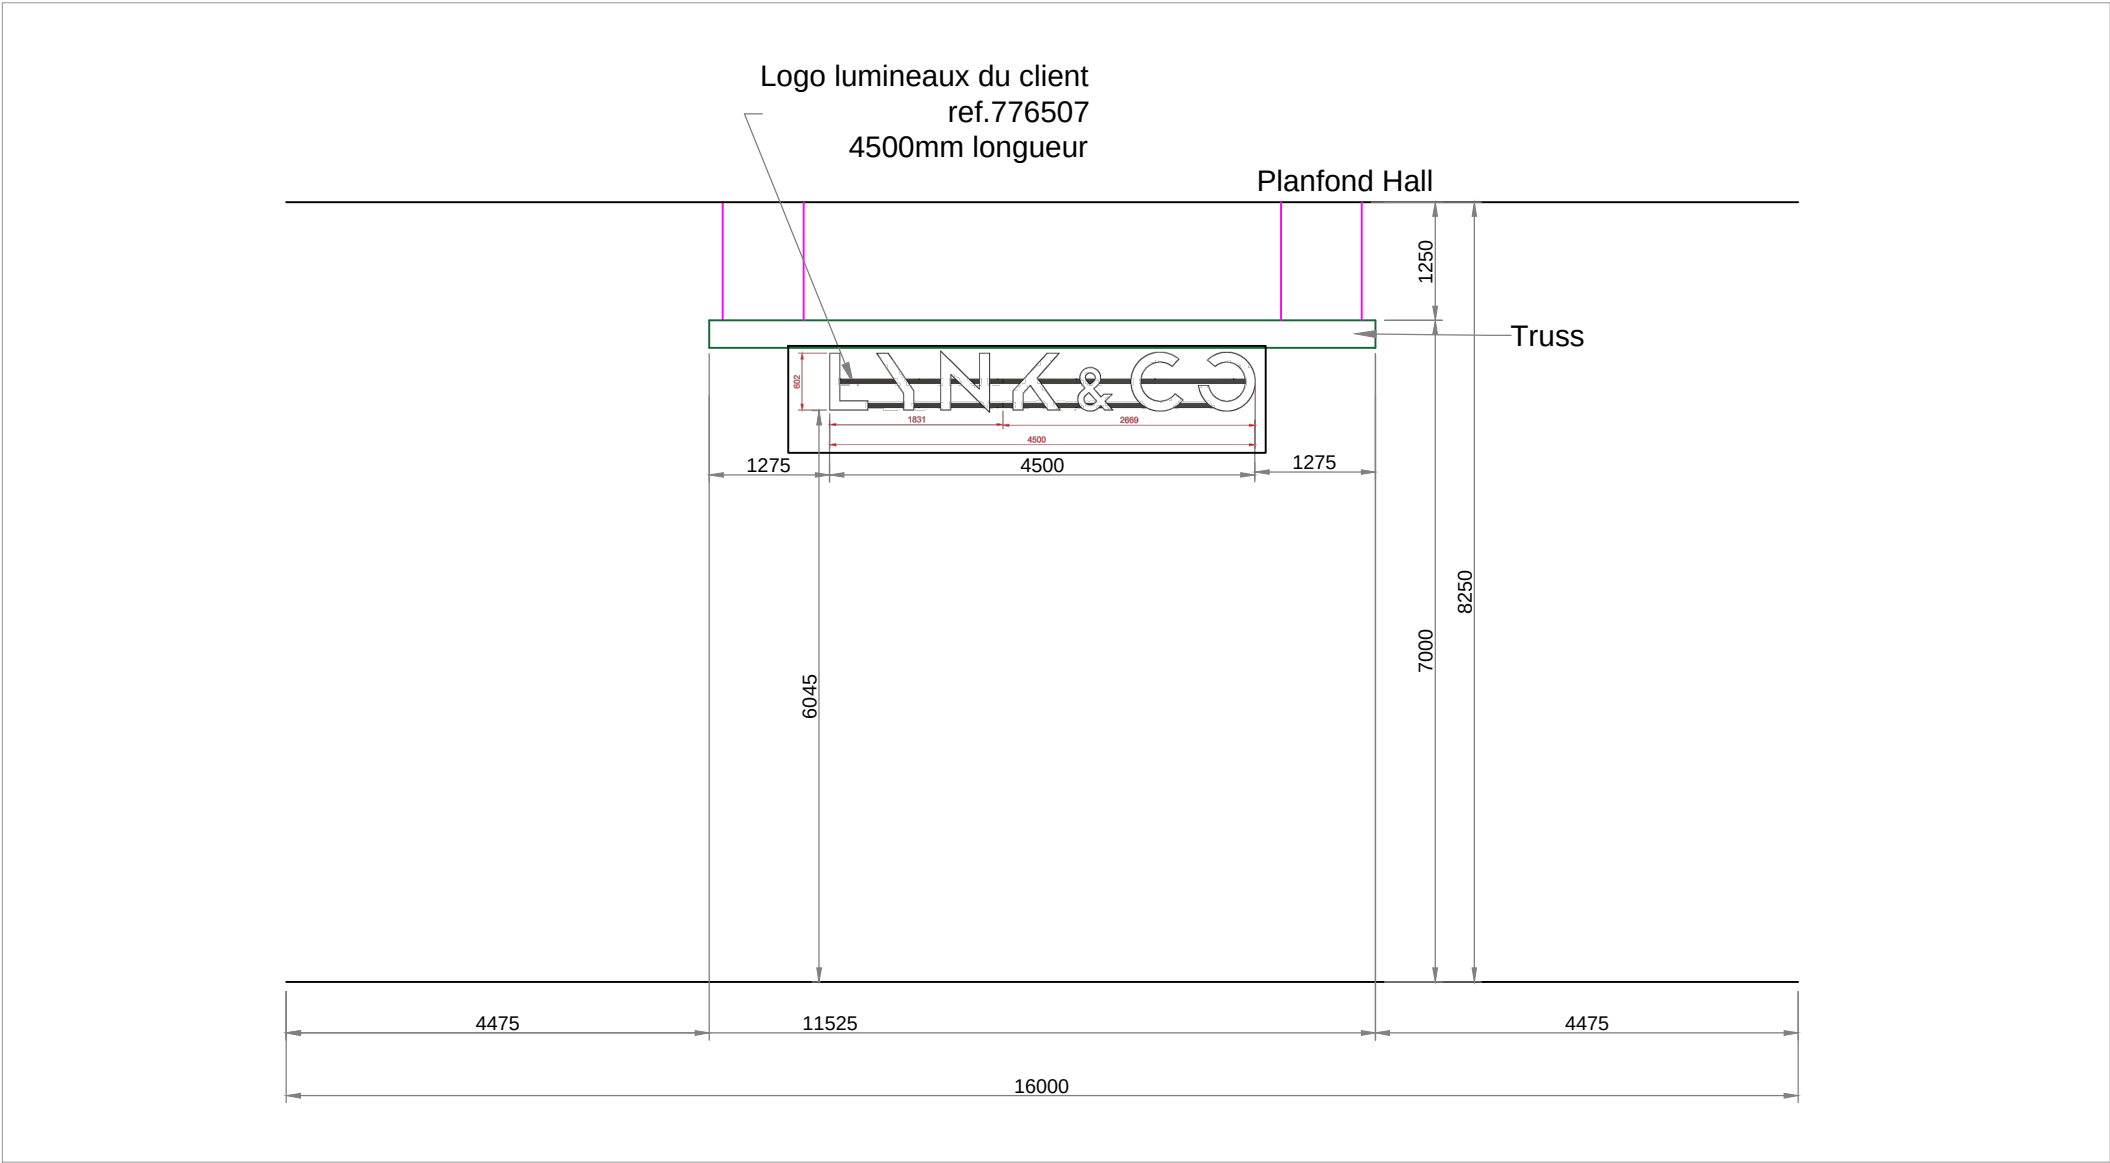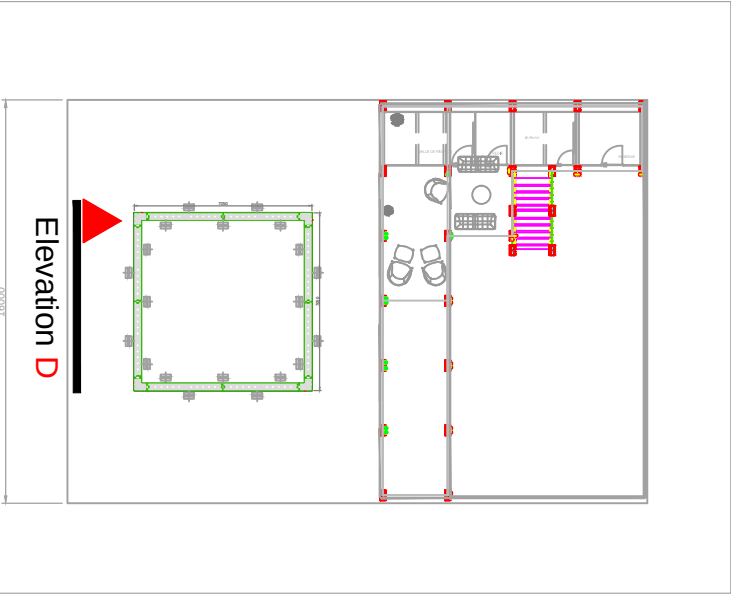

ELEVATION D





108 avenue Henri Barbusse
92600 Asnières-sur-Seine, France

Nom de stand: **LYNK & CO**
Numéro de stand: 51 A 32
Surface: **368m2**

LYNK & CO / DESSIN TECHNIQUE	
ELEVATION D	
Le Mondial de l'Auto, 2026	Dates de l'exposition : 12-18 oCTOBRE 2026
	Porte de Versailles/ Hall-5.1

ALLÉE
(Côté du Stand Tesla)

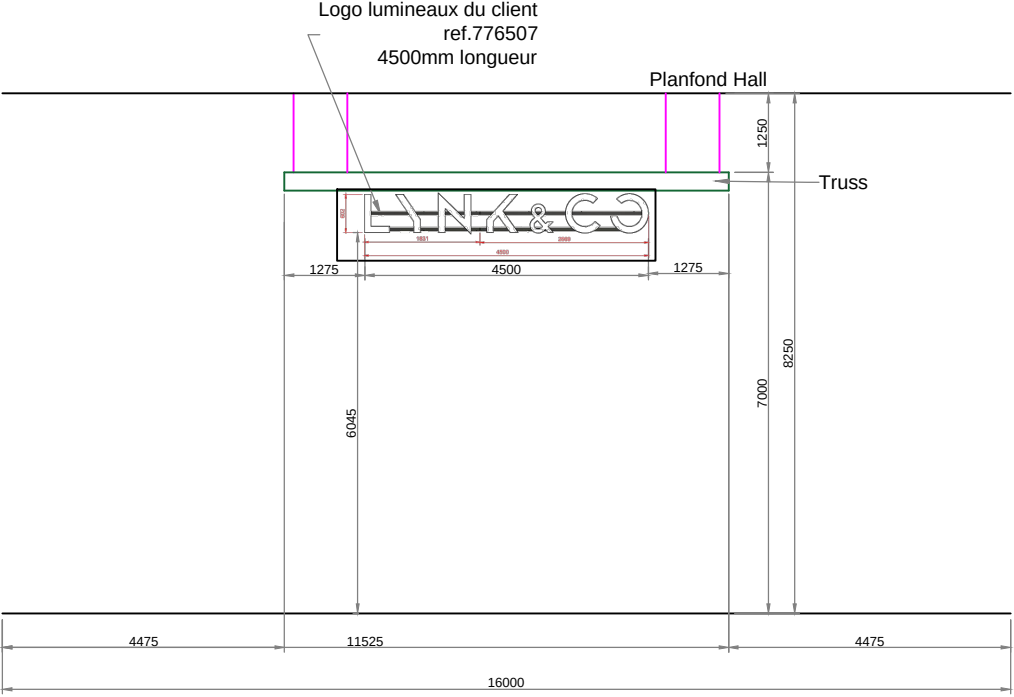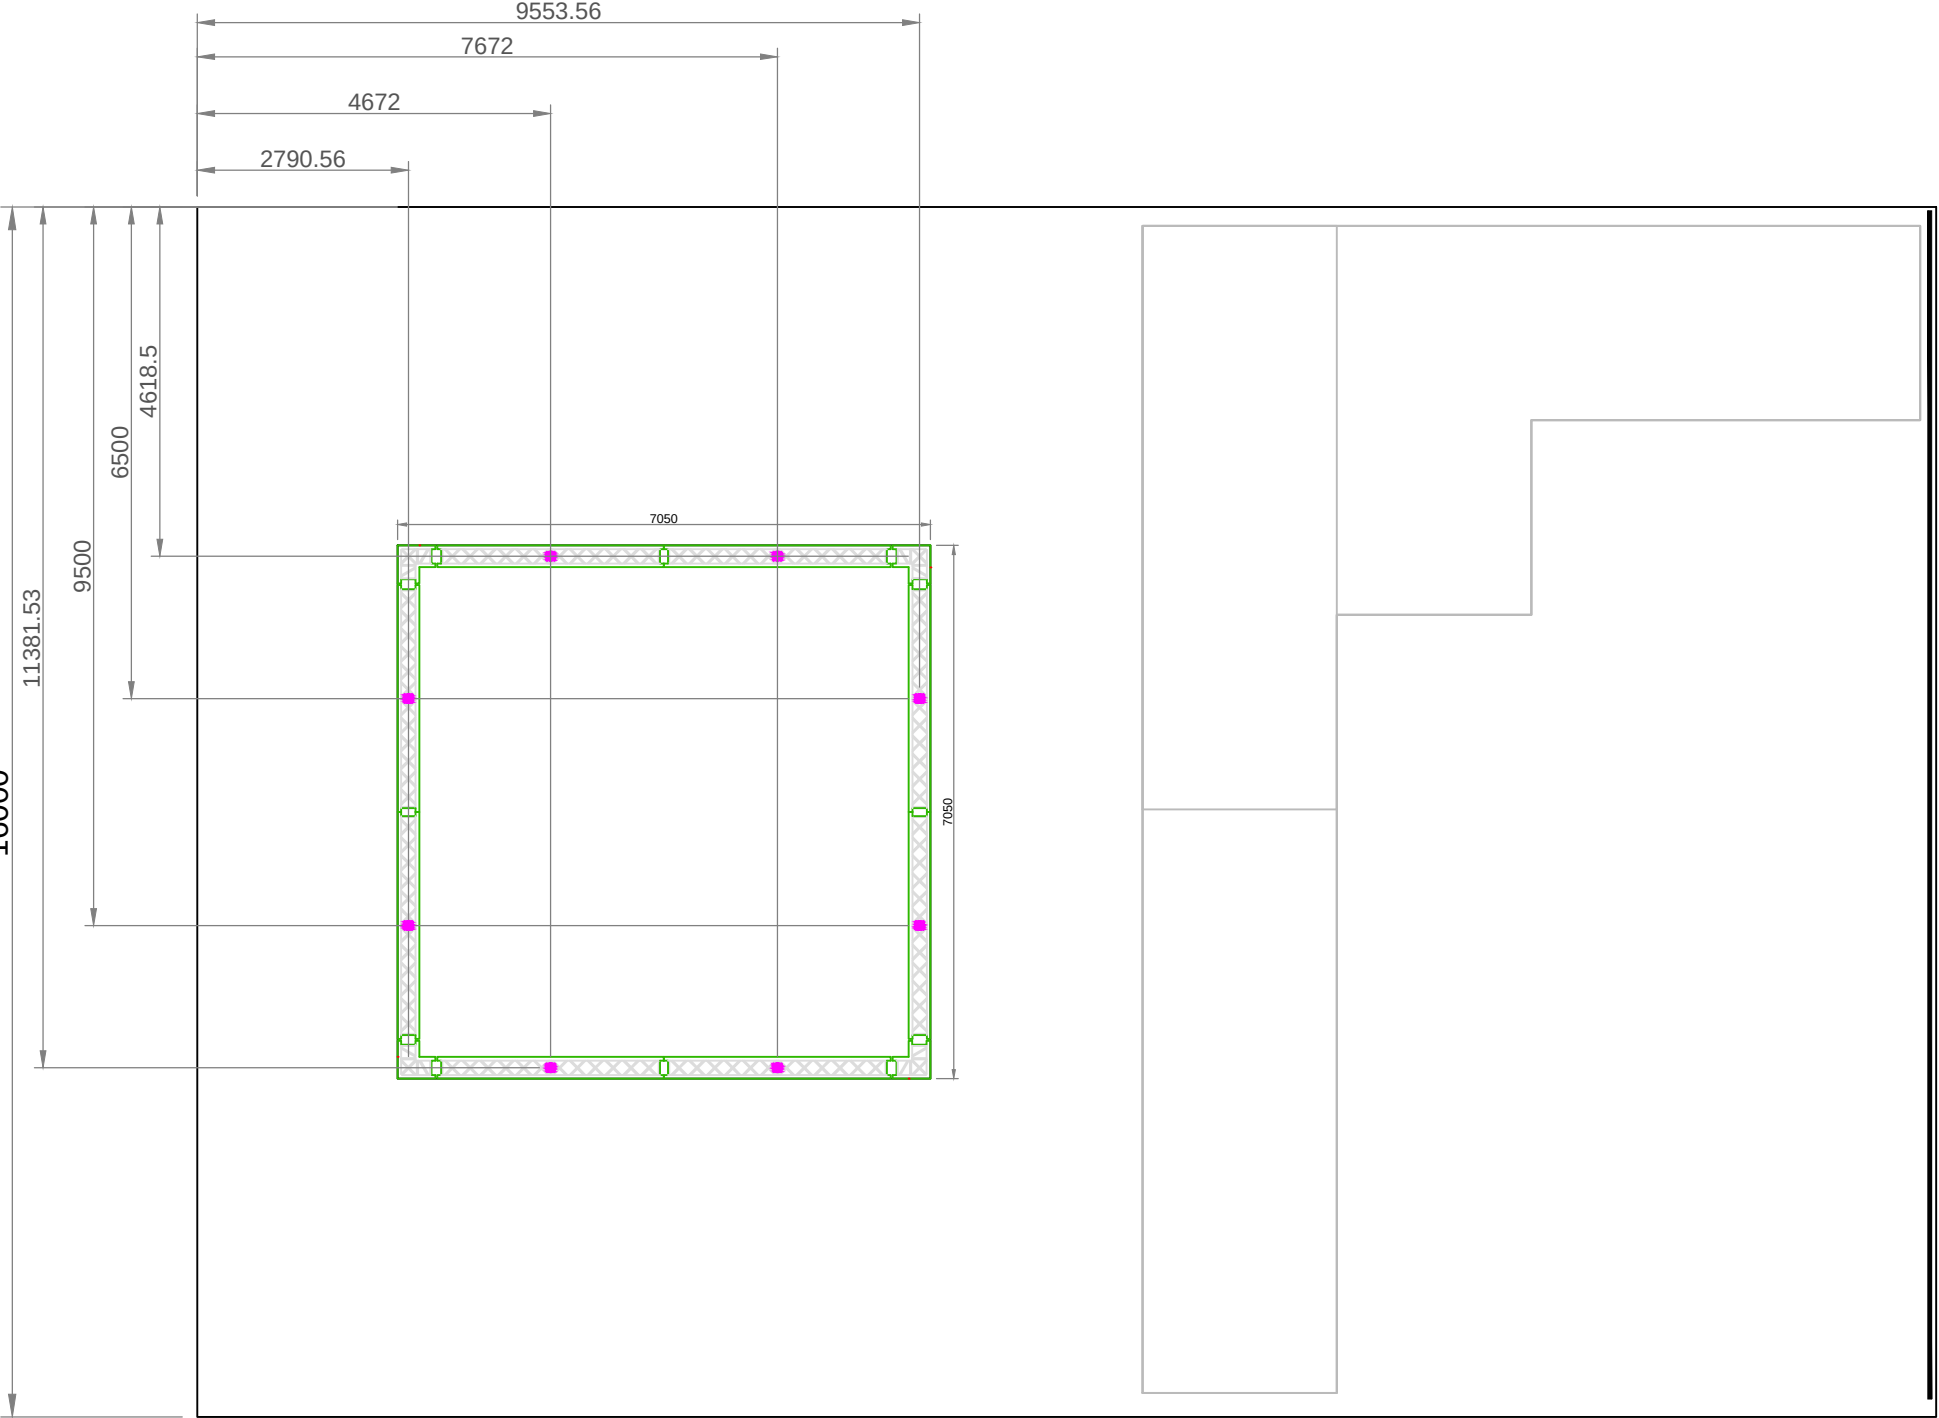

Elevation

INFORMATIONS DE SUSPENSION:

8x Point élingues

Poids total structure
+ projecteurs
+ logo lumineux : du client

Nombre de points d'élingage : 8

Charge théorique par point :
56.25 kg (≈57 kg)

Longueur des élingues :1250 mm

Hauteur structure : 7000 mm

ALLÉE
(Côté du Stand Electric box)

ALLÉE

16000

ALLÉE
(Côté du Stand Tesla)

13443

565

637

6141

60 kw Coffret
permanent

alimentation
aérienne 4 à 9kW

7050

7050

ALLÉE
(Côté du Stand Electric box)

ALLÉE



108 avenue Henri Barbusse
92600 Asnières-sur-Seine, France

Nom de stand: **LYNK & CO**

Numéro de stand: 51 A 32

Surface: **368m2**

LYNK & CO / DESSIN TECHNIQUE

PLAN COFFRET ÉLECTRIQUE

Le Mondial de l'Auto, 2026

Dates de l'exposition : 12-18 oCTOBRE 2026

Porte de Versailles/ Hall-5.1

23/09/2026


Format A3

Page: 12a

Scale=1/100

Design par : Kazi Murshida KHAN

ALLÉE
(Côté du Stand Tesla)

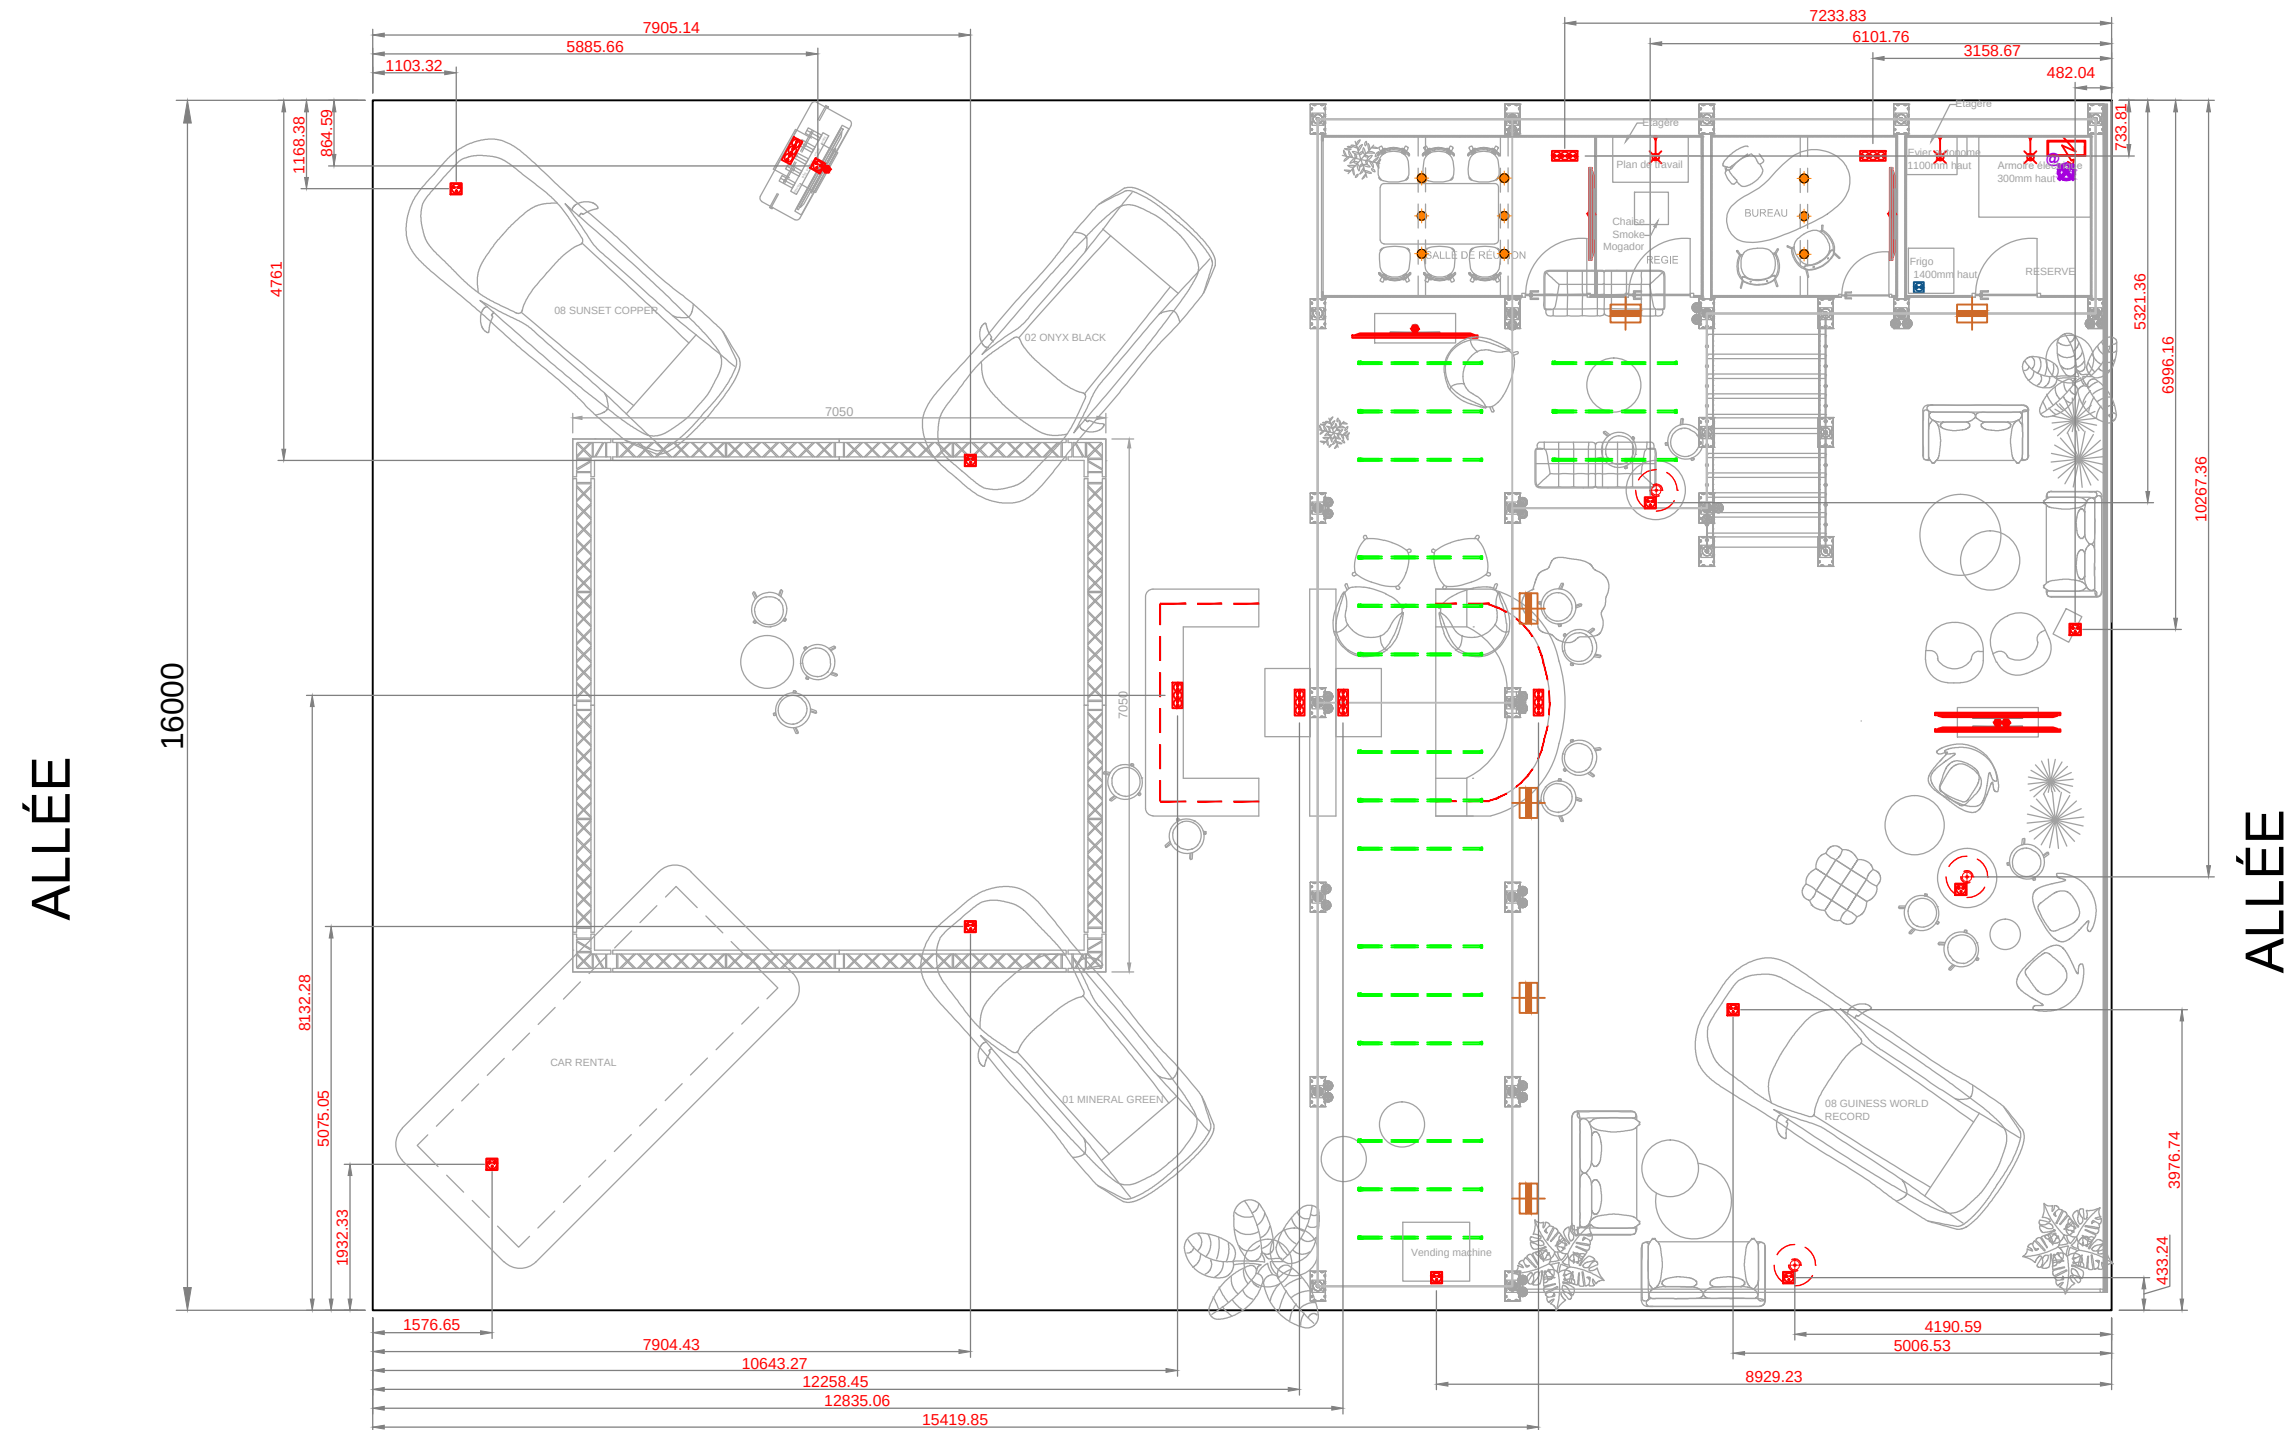

ALLÉE
(Côté du Stand Electric box)

LISTE ÉLECTRIQUE

	TABLEAU ÉLECTRIQUE	1
	Arrivée électrique aérienne	1
	TRIPLETTE	7
	PRISE ECRAN	6
	PRISE alim	11
	Frigo 140L	1
	Projecteur	6
	SPOT à tige led -Truss	20
	Tube néon LED vert	18
	Écran LED Transparent	1
	Spot	9
	Mbps	1
	Lampadaire	3

ALLÉE

16000

ALLÉE
(Côté du Stand Tesla)


ALLÉE

ALLÉE
(Côté du Stand Electric box)

LISTE ÉLECTRIQUE		
	1 arrivée électrique + 1 multiprise	
	PRISE alim	1
	Lampadaire	1
	Tube néon LED vert	18

ALLÉE
(Côté du Stand Tesla)

ALLÉE

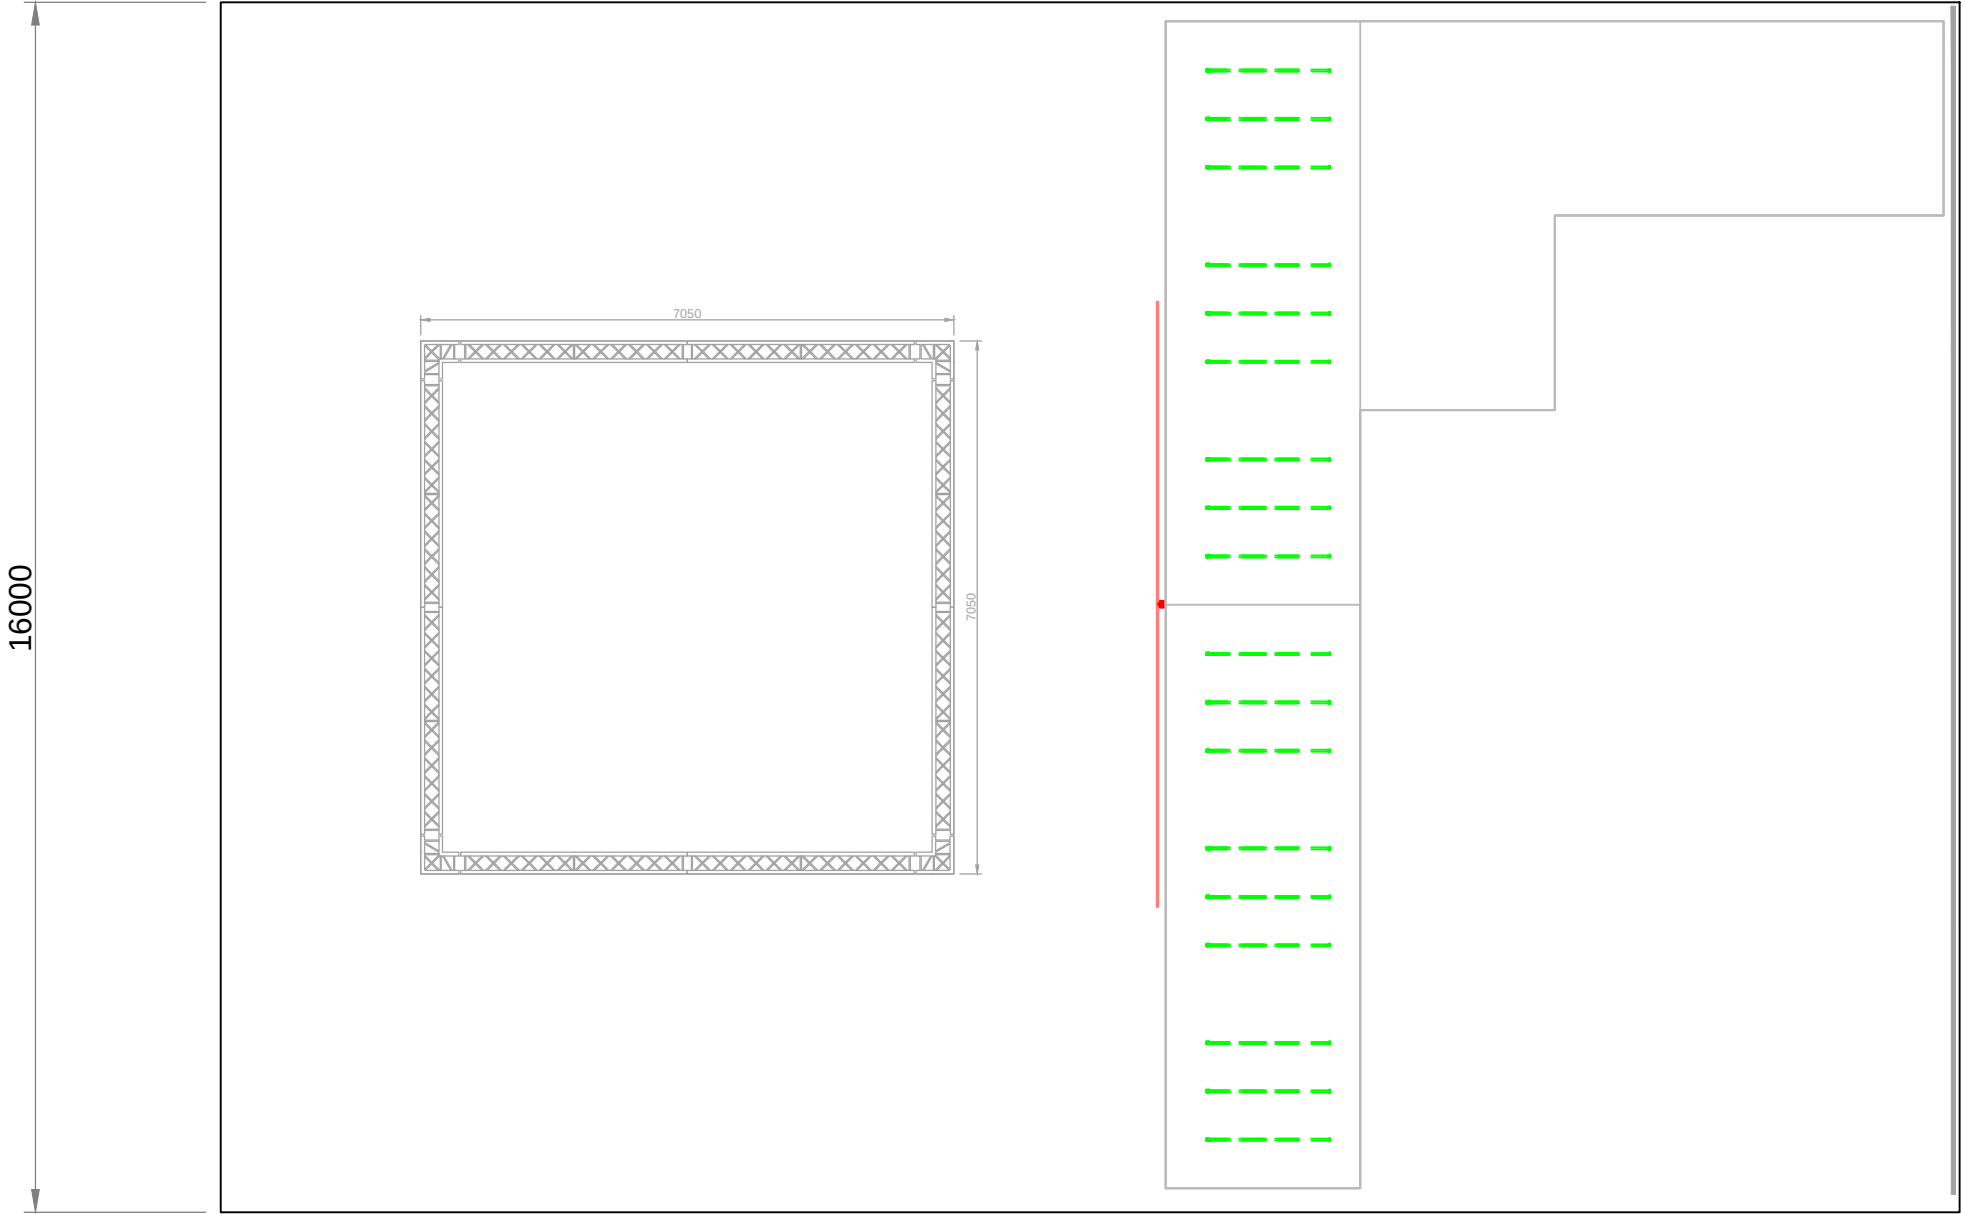

ALLÉE

ALLÉE
(Côté du Stand Electric box)

LISTE ÉLECTRIQUE

	Tube néon LED vert	18
	Écran LED Transparent	1




108 avenue Henri Barbusse
92600 Asnières-sur-Seine, France

Nom de stand: **LYNK & CO**
Numéro de stand:51 A 32
Surface: **368m2**

LYNK & CO / DESSIN TECHNIQUE		23/09/2026	Page: 12c
PLAN ÉLECTRIQUE 2 etage		Format A3	Scale=1/100
Le Mondial de l'Auto, 2026	Dates de l'exposition : 12-18 oCTOBRE 2026	Design par : Kazi Murshida KHAN	
	Porte de Versailles/ Hall-5.1		

ALLÉE
(Côté du Stand Tesla)

ALLÉE

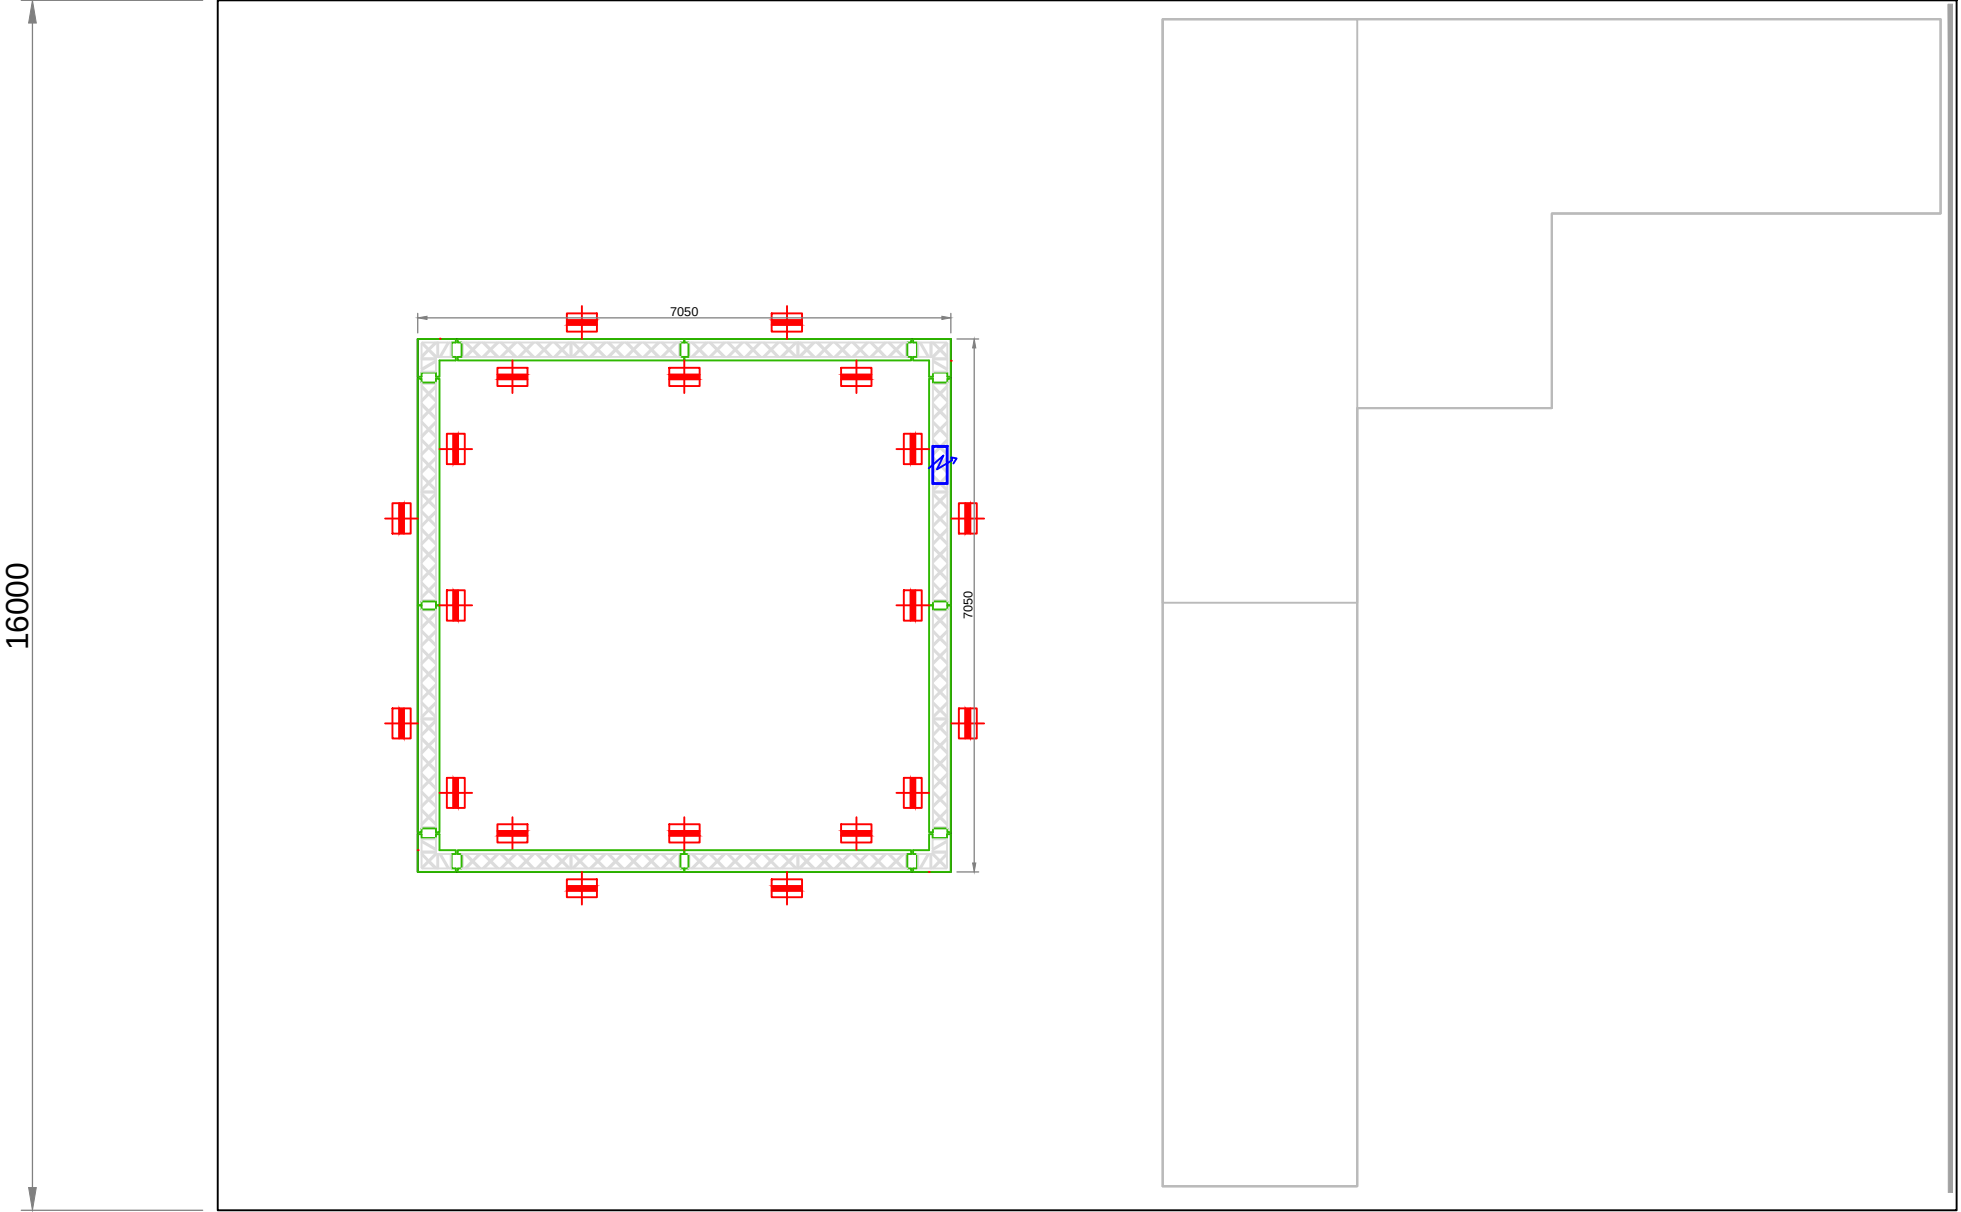

ALLÉE

	Arrivée électrique aérienne	1
	SPOT à tige led -Truss	20

ALLÉE
(Côté du Stand Electric box)




108 avenue Henri Barbusse
92600 Asnières-sur-Seine, France

Nom de stand: **LYNK & CO**
Numéro de stand:51 A 32
Surface: **368m2**

LYNK & CO / DESSIN TECHNIQUE		23/09/2026	Page: 12d
PLAN ÉLECTRIQUE Truss		Format A3	Scale=1/100
Le Mondial de l'Auto, 2026	Dates de l'exposition : 12-18 oCTOBRE 2026	Design par : Kazi Murshida KHAN	
	Porte de Versailles/ Hall-5.1		

ALLÉE
(Côté du Stand Tesla)

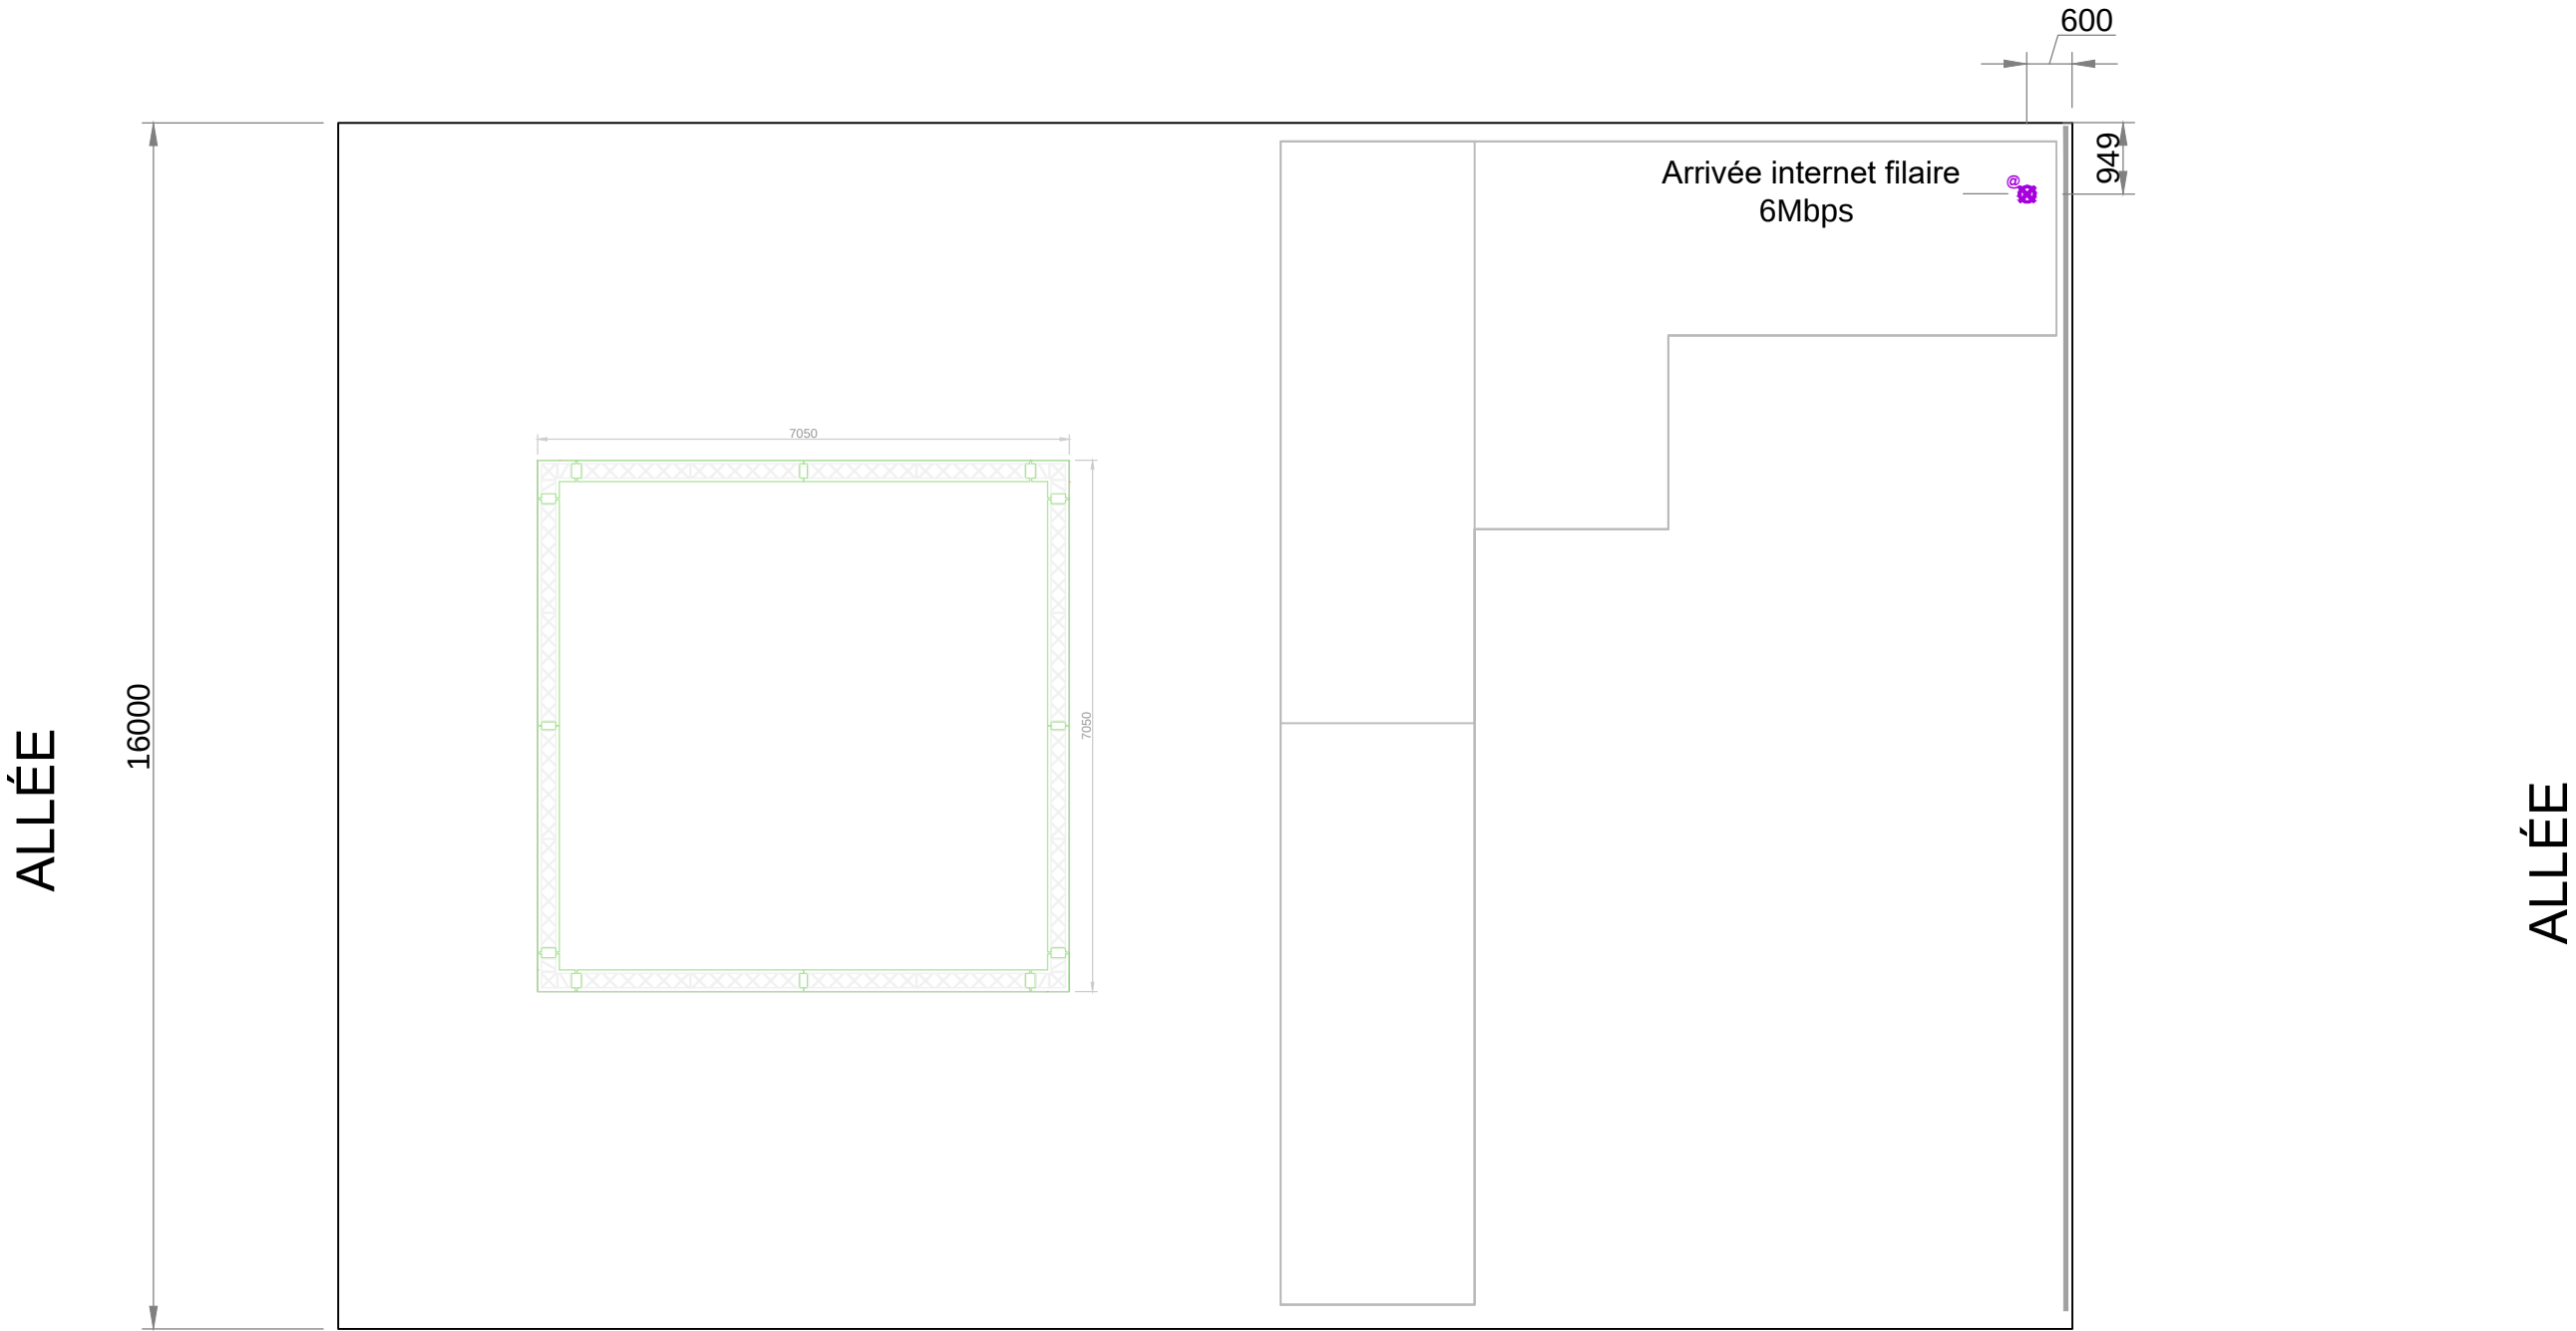

ALLÉE
(Côté du Stand Electric box)




108 avenue Henri Barbusse
92600 Asnières-sur-Seine, France

Nom de stand: **LYNK & CO**
Numéro de stand: 51 A 32
Surface: **368m2**

LYNK & CO / DESSIN TECHNIQUE		23/09/2026	Page: 12e
PLAN INTERNET		Format A3	Scale=1/100
Le Mondial de l'Auto, 2026	Dates de l'exposition : 12-18 oCTOBRE 2026		Design par : Kazi Murshida KHAN
	Porte de Versailles/ Hall-5.1		

ALLÉE
(Côté du Stand Tesla)

ALLÉE

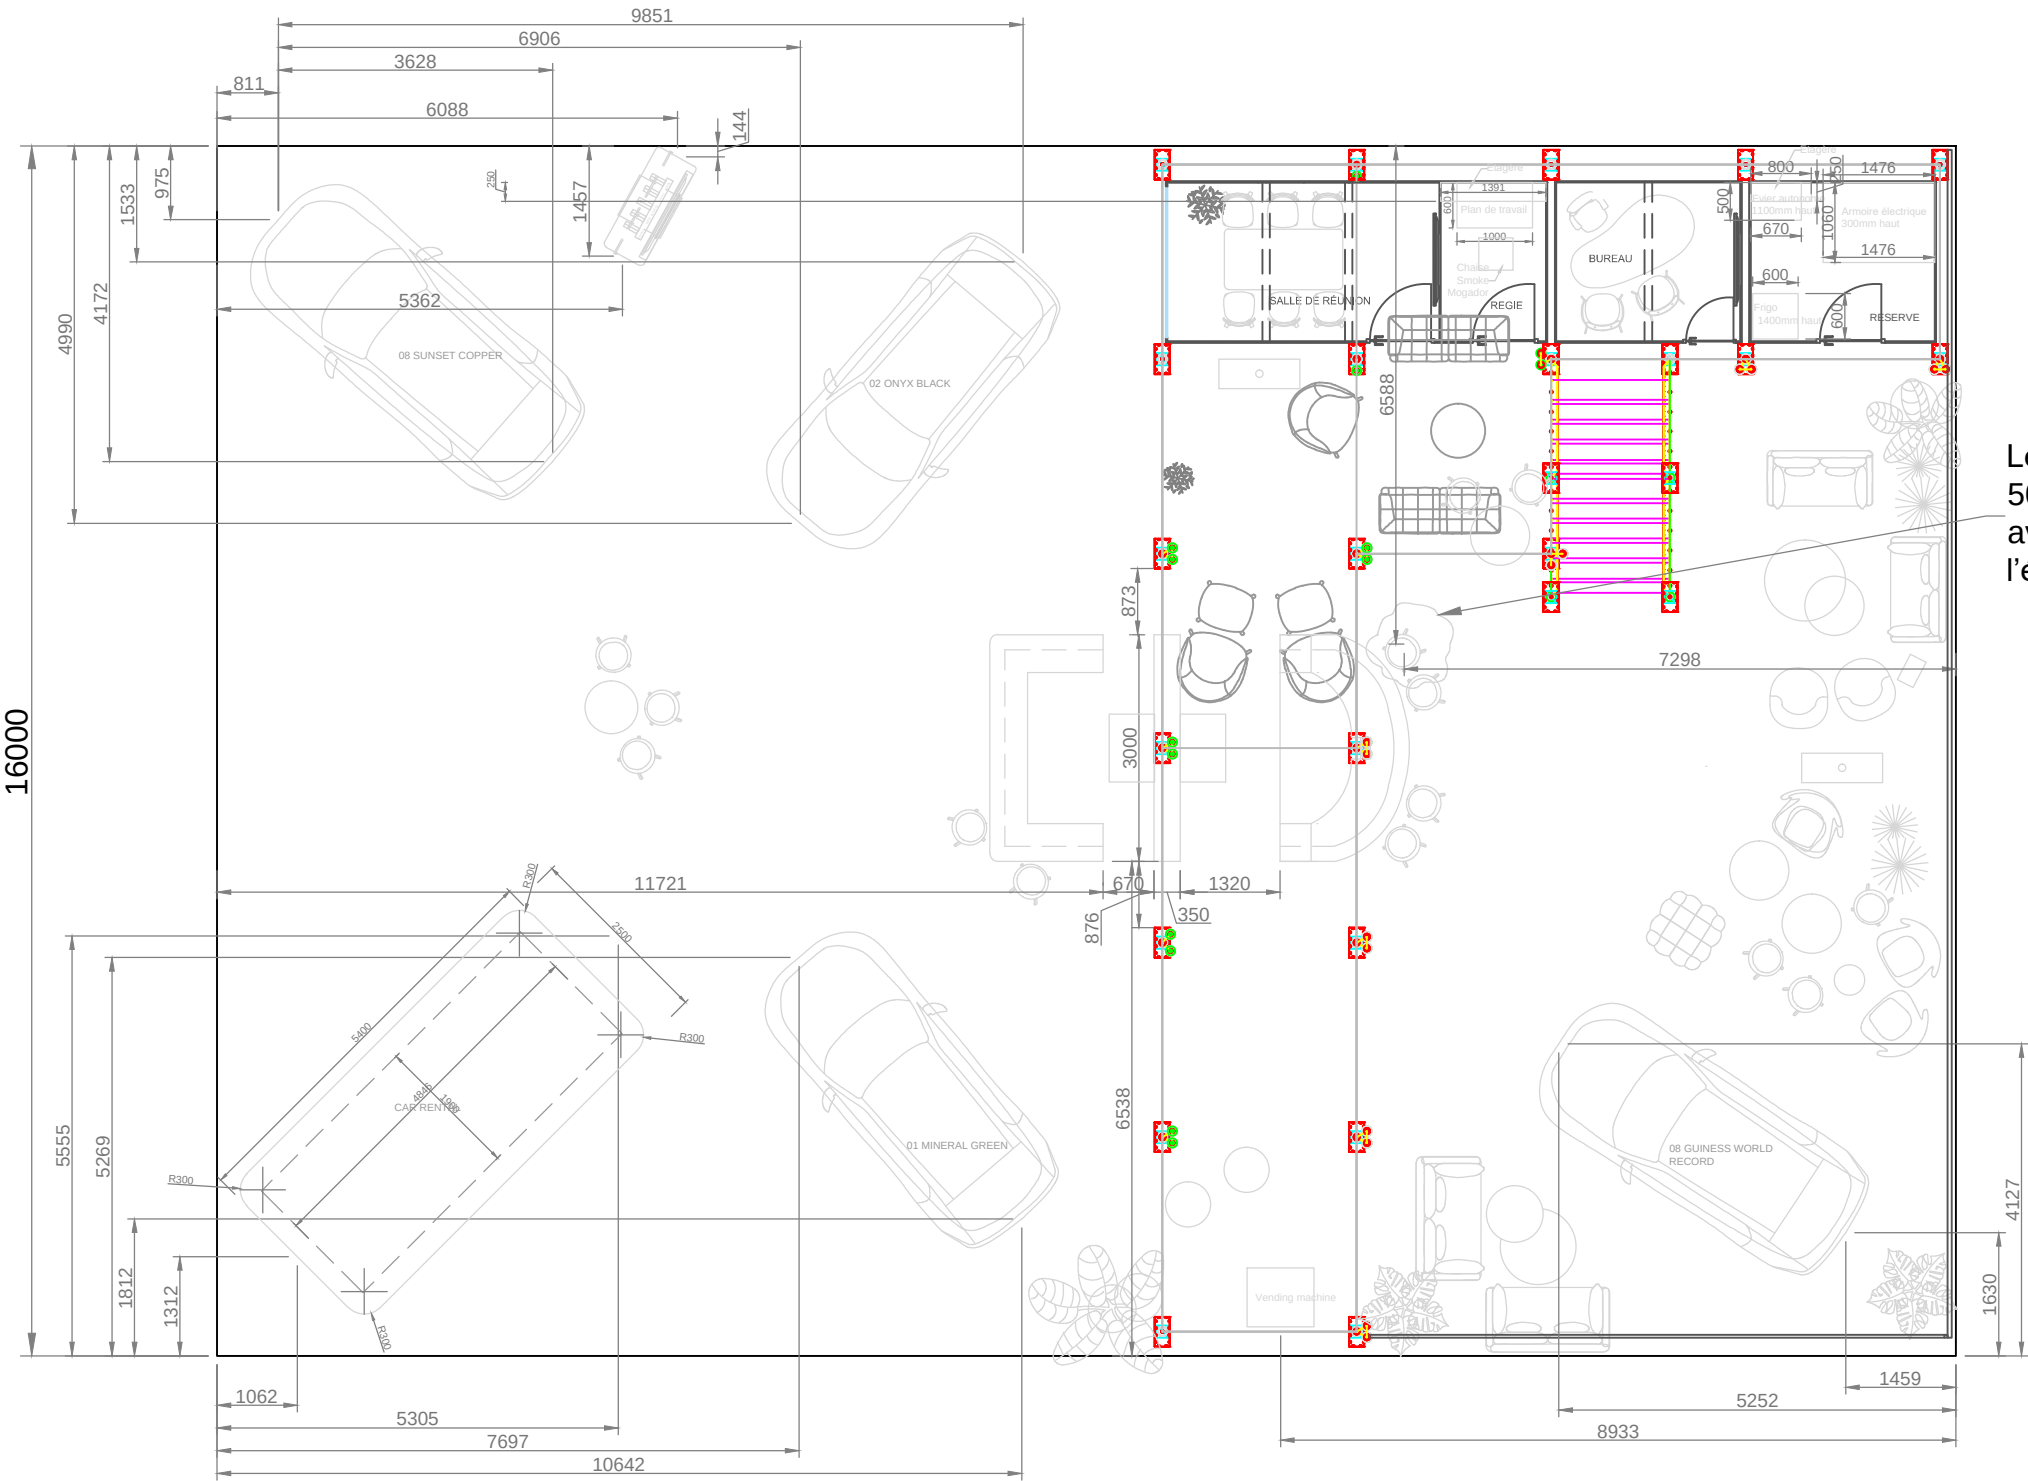

Le nuage à suspendre environ 50kg. avec 1 bras depuis l'échafaudage

ALLÉE

ALLÉE
(Côté du Stand Electric box)



108 avenue Henri Barbusse
92600 Asnières-sur-Seine, France

Nom de stand: **LYNK & CO**
Numéro de stand: 51 A 32
Surface: **368m2**

Le Mondial de l'Auto, 2026

LYNK & CO / DESSIN TECHNIQUE

PLAN position meuble et voiture RDC

Dates de l'exposition : 12-18 OCTOBRE 2026

Porte de Versailles/ Hall-5.1



23/09/2026

Format A3


Design par : Kazi Murshida KHAN

Page: 13

Scale=1/100

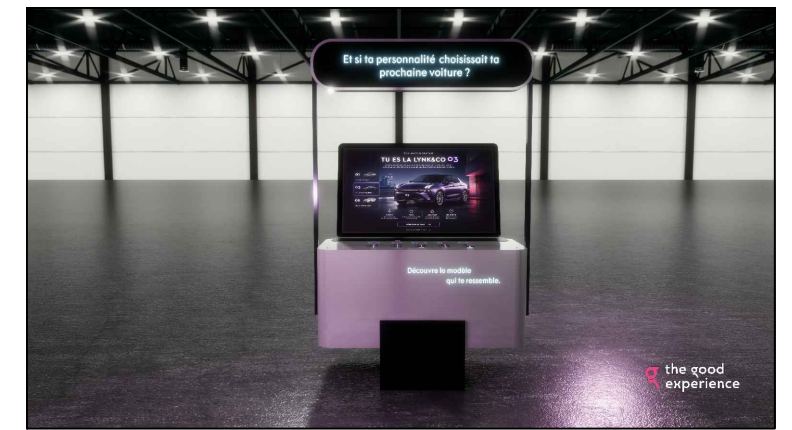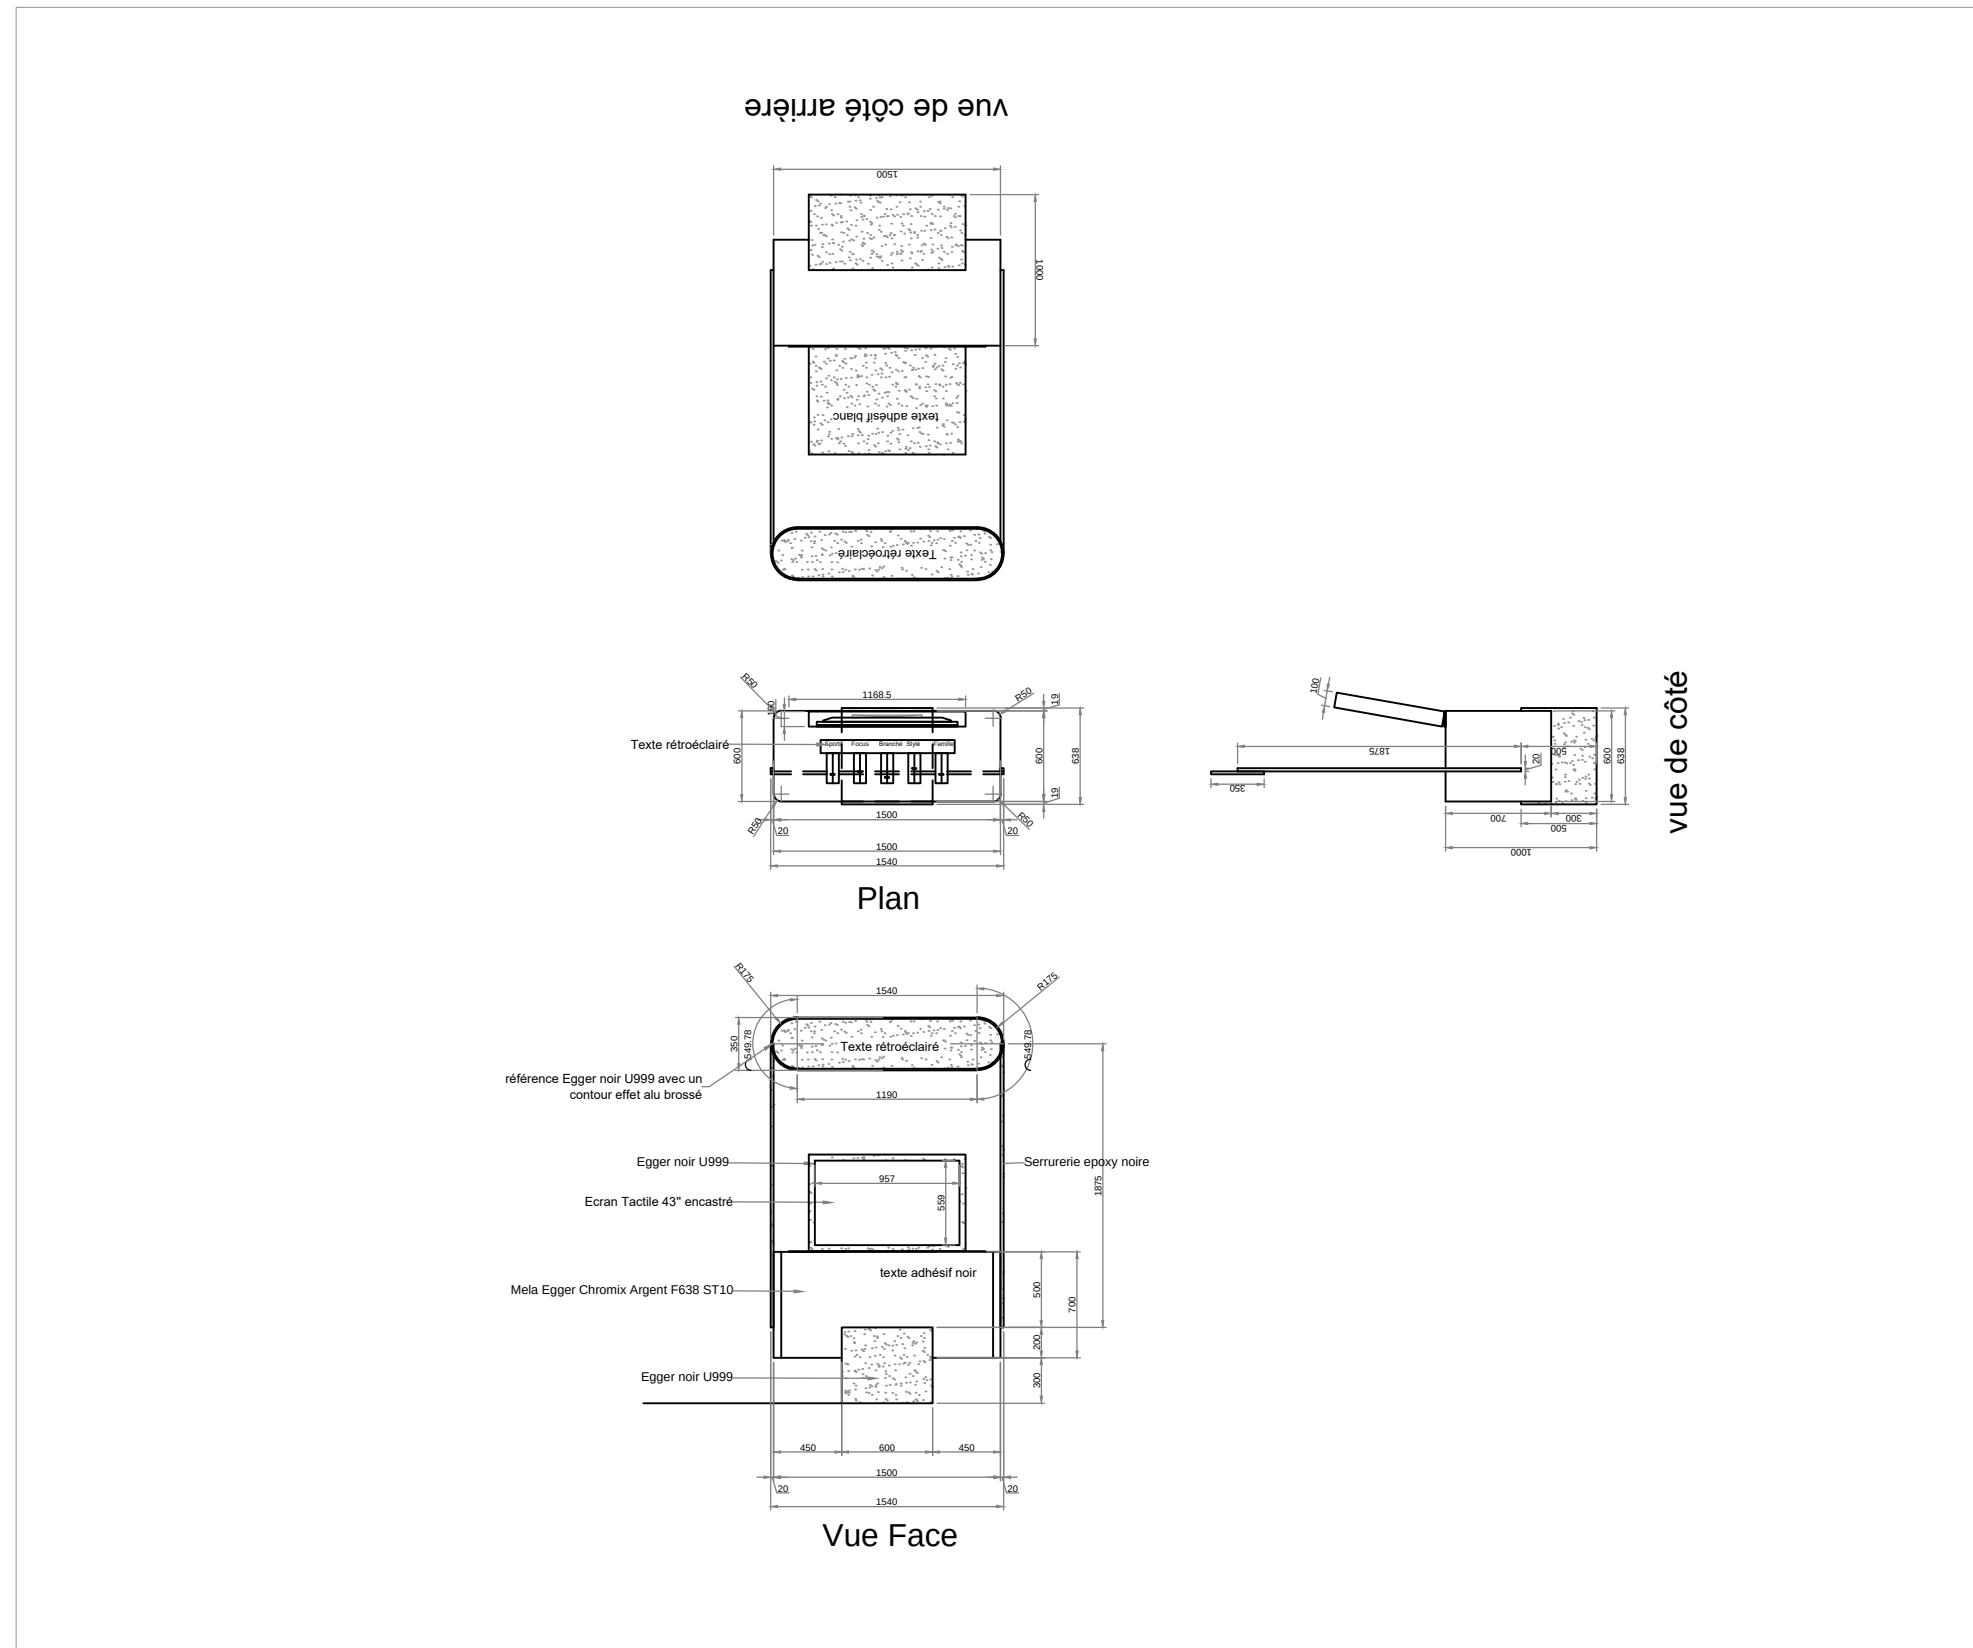


Vue Face

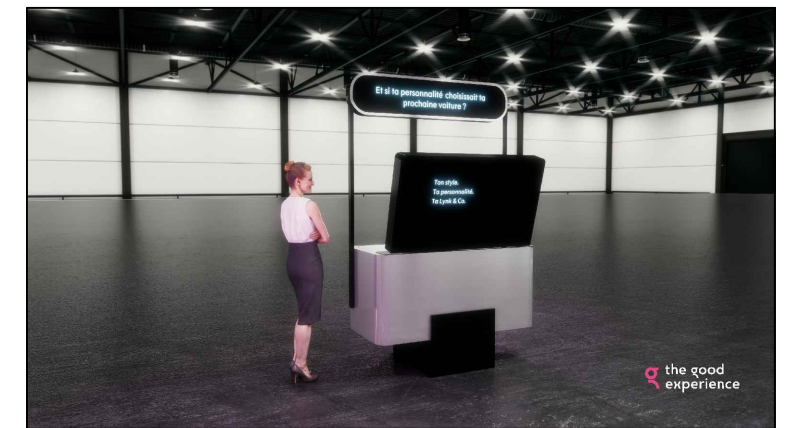

Vue arrière



Vue de côté

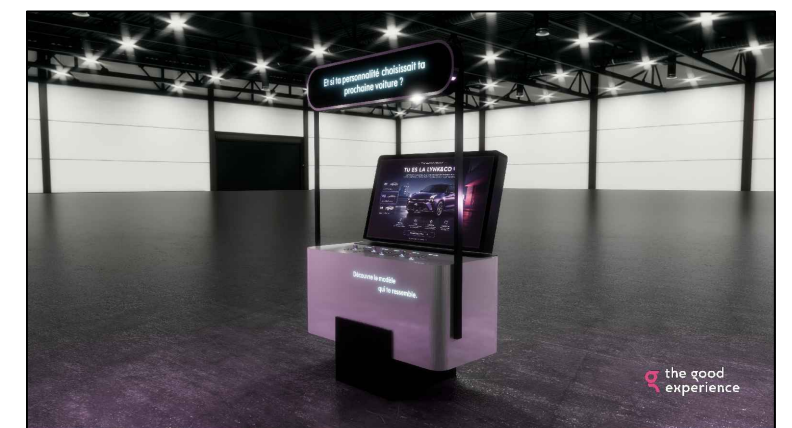

Vue de côté